


The Jing-Zhang public space spine is now continuous; the lateral public relationship with the cities on either side is not.

Not five points along the line, but a reorganisation of the relationship between one spine and the city: five transects identify the recurring problems, and the response windows for the three key areas carry the focused response.

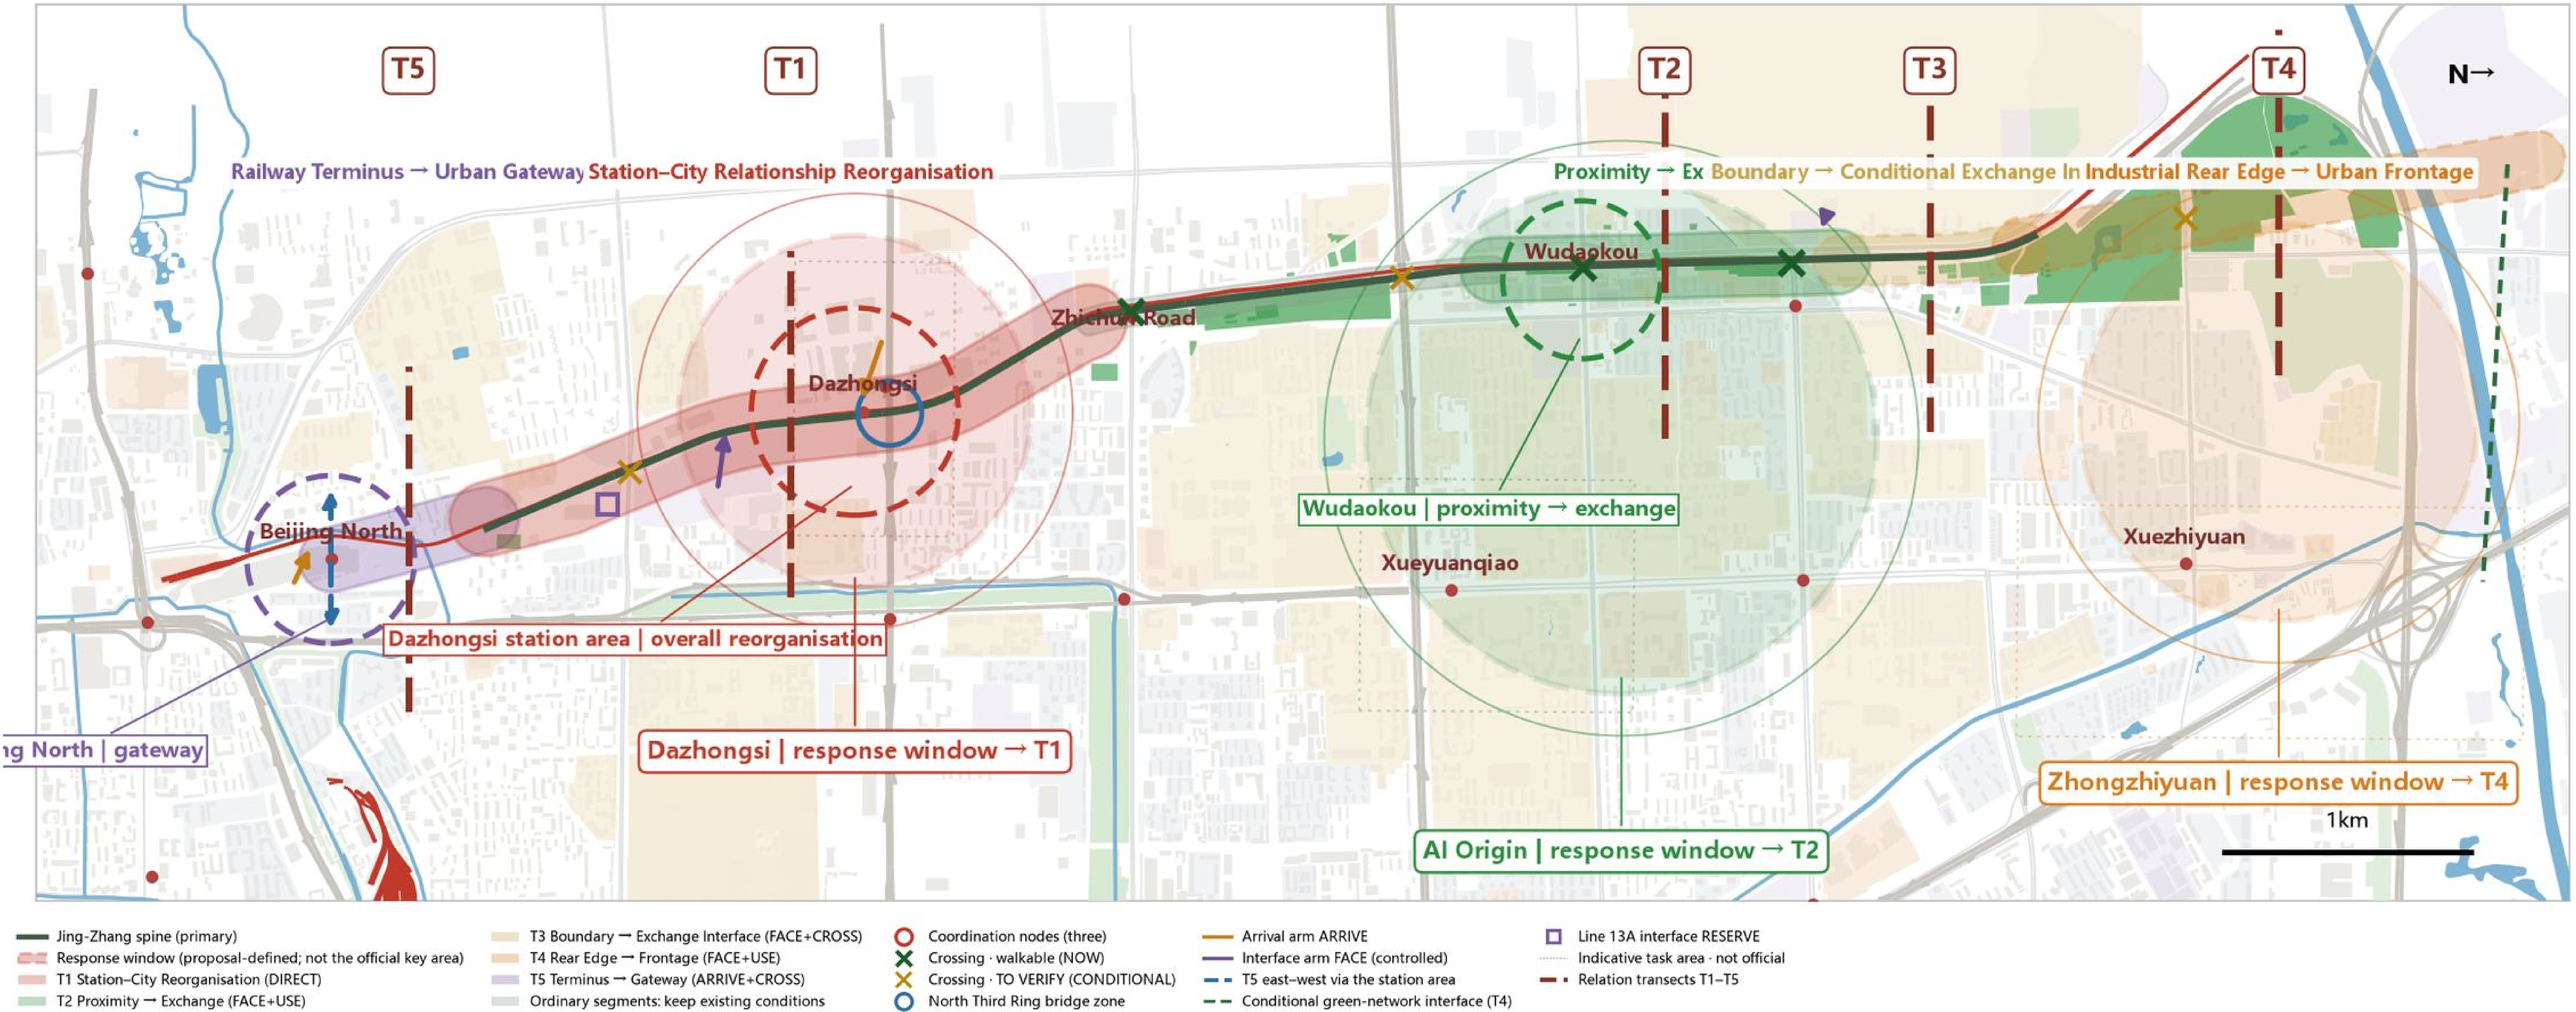

The three rings on the plan are the response windows identified by this proposal along Jing-Zhang; not equivalent to the official key-area extent.

Three-System Synthesis | GRAY × SOCIAL × GREEN



The three infrastructure deficits overlap in different combinations, producing a different urban relation problem at each of the five transects T1-T5.

Five Urban Relation Transects | Index

- T1 Station-City Relationship Reorganisation**
Dazhongsi
- T2 Proximity → Exchange**
Chengfu Road-Wudaokou
- T3 Boundary → Conditional Exchange Interface**
Tsinghua East-Xueyuan Road
- T4 Industrial Rear Edge → Urban Frontage**
Zhongzhiyuan
- T5 Railway Terminus → Urban Gateway**
Beijing North Railway Station

ARRIVEFACECROSS

FACEUSE

FACECROSS

FACEUSE

ARRIVECROSS

Transects are design units, not zoning districts; T1 is taken to object level on the Key Areas board.

Renewal is not about redrawing parcels, but about reorganising functions, interfaces and public exchange relationships.

Assuming neither large-scale demolition nor statutory land-use change, this board answers how innovation exchange can be built inside the existing urban fabric through functional organisation, public space, ground-floor interfaces and operation.

T2 | Proximity → Exchange


Chengfu Road–Wudaokou

FACE

USE



EXISTING URBAN RELATIONS

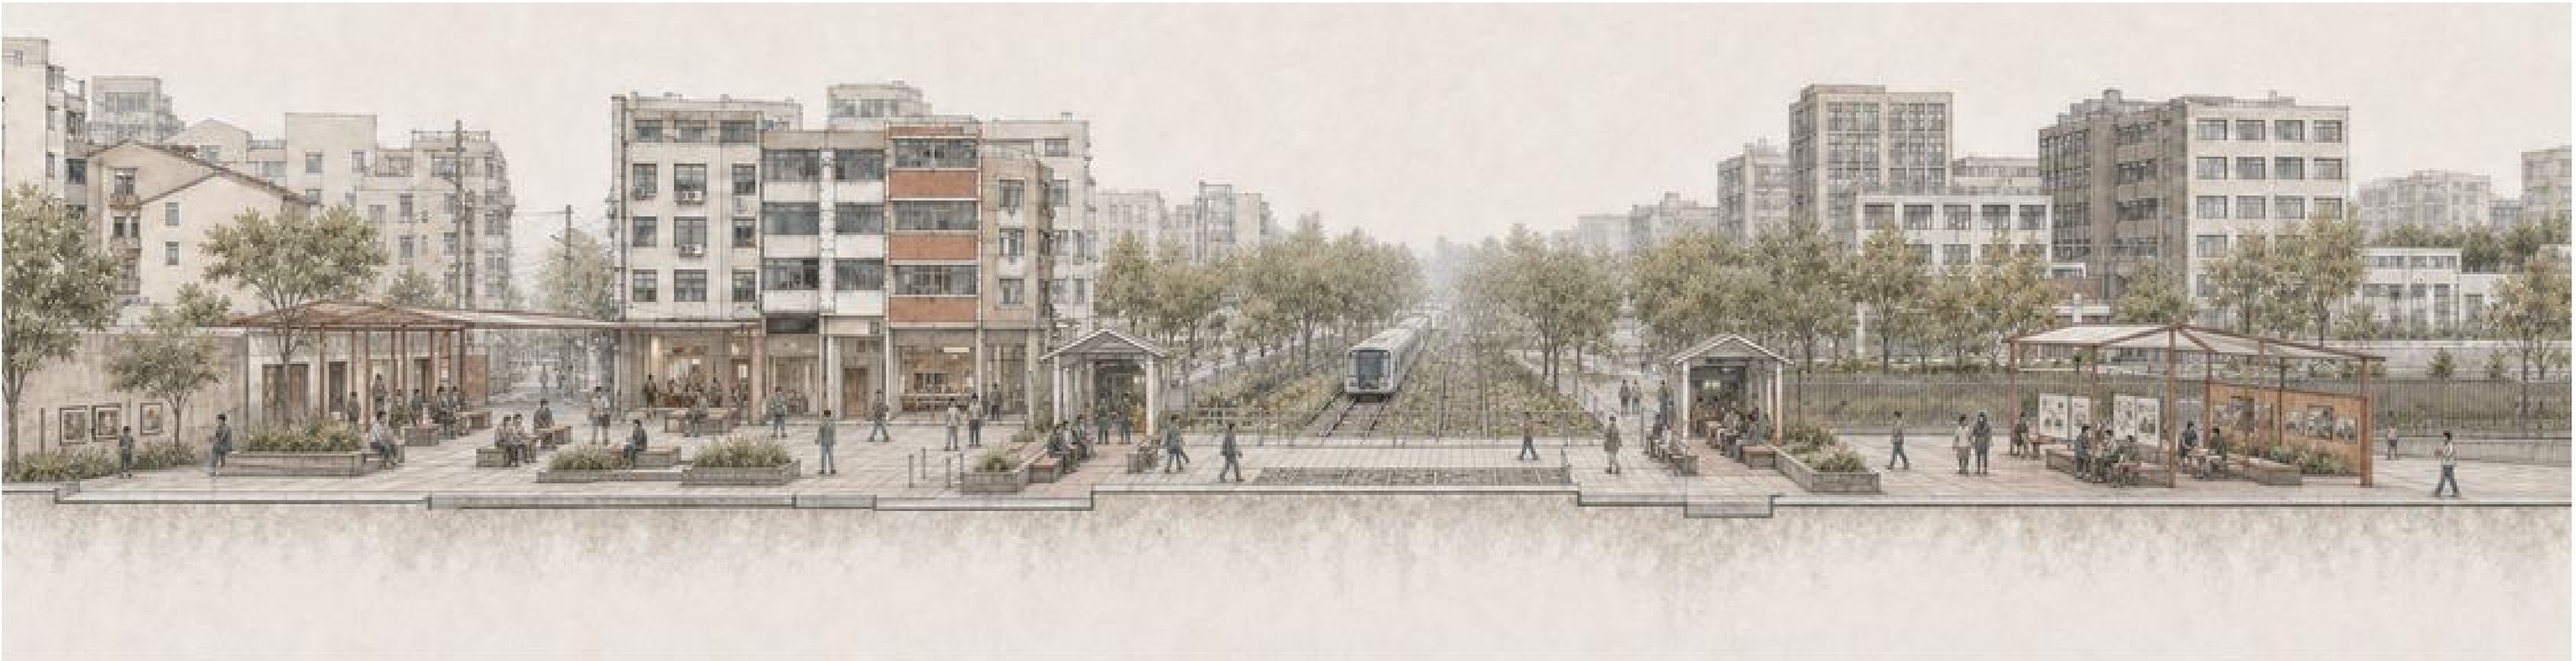

FUTURE RELATION SCENARIO

Existing | community — passing by — existing crossing — passing by — universities / innovation resources Future | community exchange — arrival across the corridor — managed innovation exchange

T3 | Boundary → Conditional Exchange Interface

Tsinghua East–Xueyuan Road

FACE

CROSS



EXISTING URBAN RELATIONS



FUTURE RELATION SCENARIO


Existing | a single hard boundary Future | layered, controlled exchange interface: closed but publicly oriented — semi-open exchange — conditionally controlled opening; opening locations are design-defined and do not correspond to existing campus gates.

Four Renewal Modes

- DIRECT DESIGN**
public space, ground-floor interfaces, arrival organisation
- PLANNING CONTROL**
interface control guidelines, conditional openings
- MANAGEMENT / OPERATION**
time-shared use, opening hours, programme organisation
- KEEP / NO DESIGN**
no fence removal, no forced opening — also a planning decision

All four modes coexist within the same block; which mode applies where is itself part of the planning decision.

SOCIAL evidence | resources are clustered; exchange interfaces and openness are not continuous

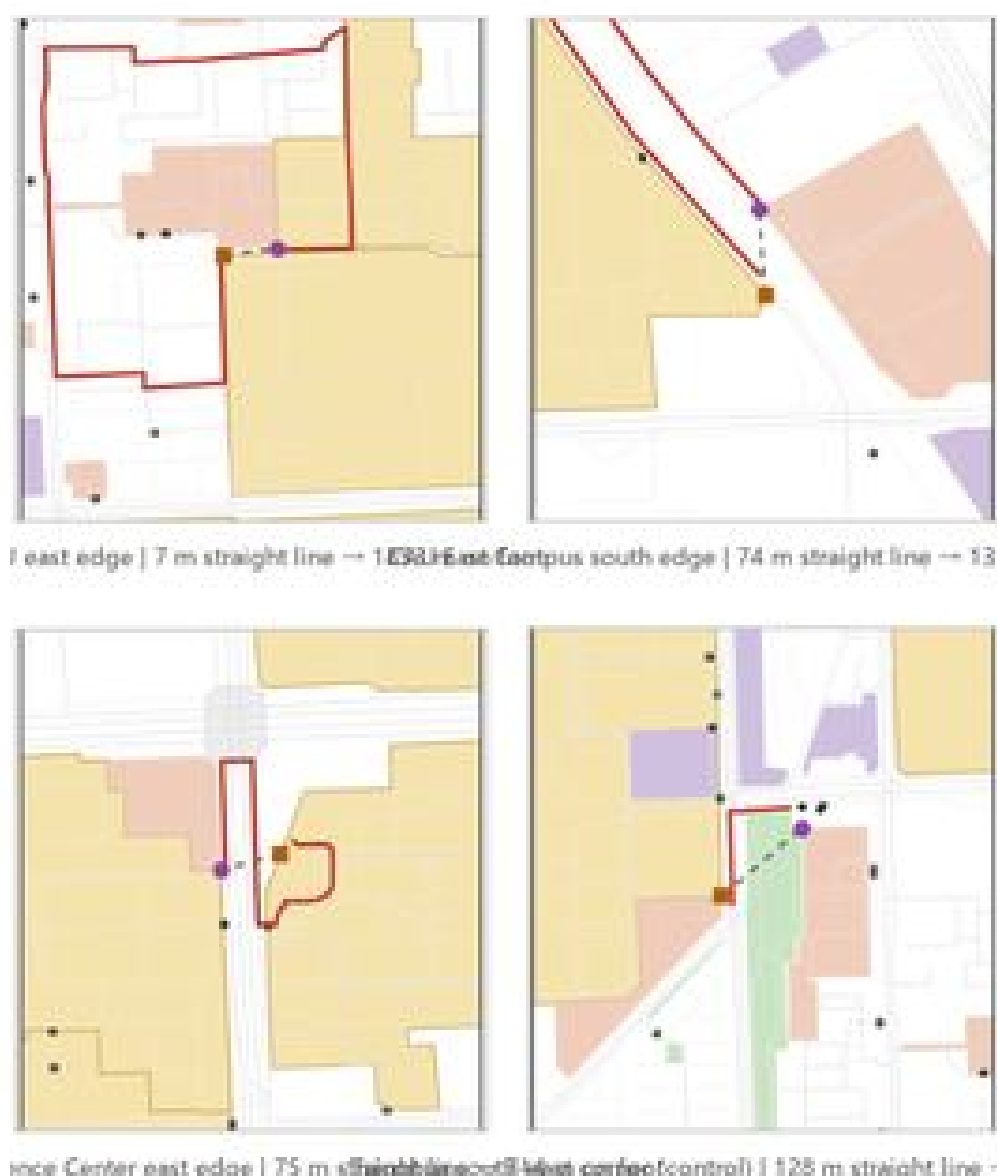

Campus boundary | detour length is set by gate location.



SOCIAL system structure | universities / innovation resources · communities / everyday services · functional relations in the built area.

In a built-up area, what can be designed is the relationship, not the parcel.

Resources already clustered

Universities, research, translation services, industrial parks and everyday services are densely clustered along the corridor.

Weak exchange interface

Public space is the most direct potential interface between them, and it is the weakest layer.


The mismatch is in real walking

Facilities are not lacking; access, openness and exchange conditions are.

A Station ≠ Real Access. Spatial Proximity ≠ Easy Access.


The transport infrastructure that supports north–south operation also forms the lateral barrier to east–west urban relations. No new rail crossing is proposed; the response is organised through station areas, arrival and gateway relationships.

GRAY system | operating spine and lateral barrier

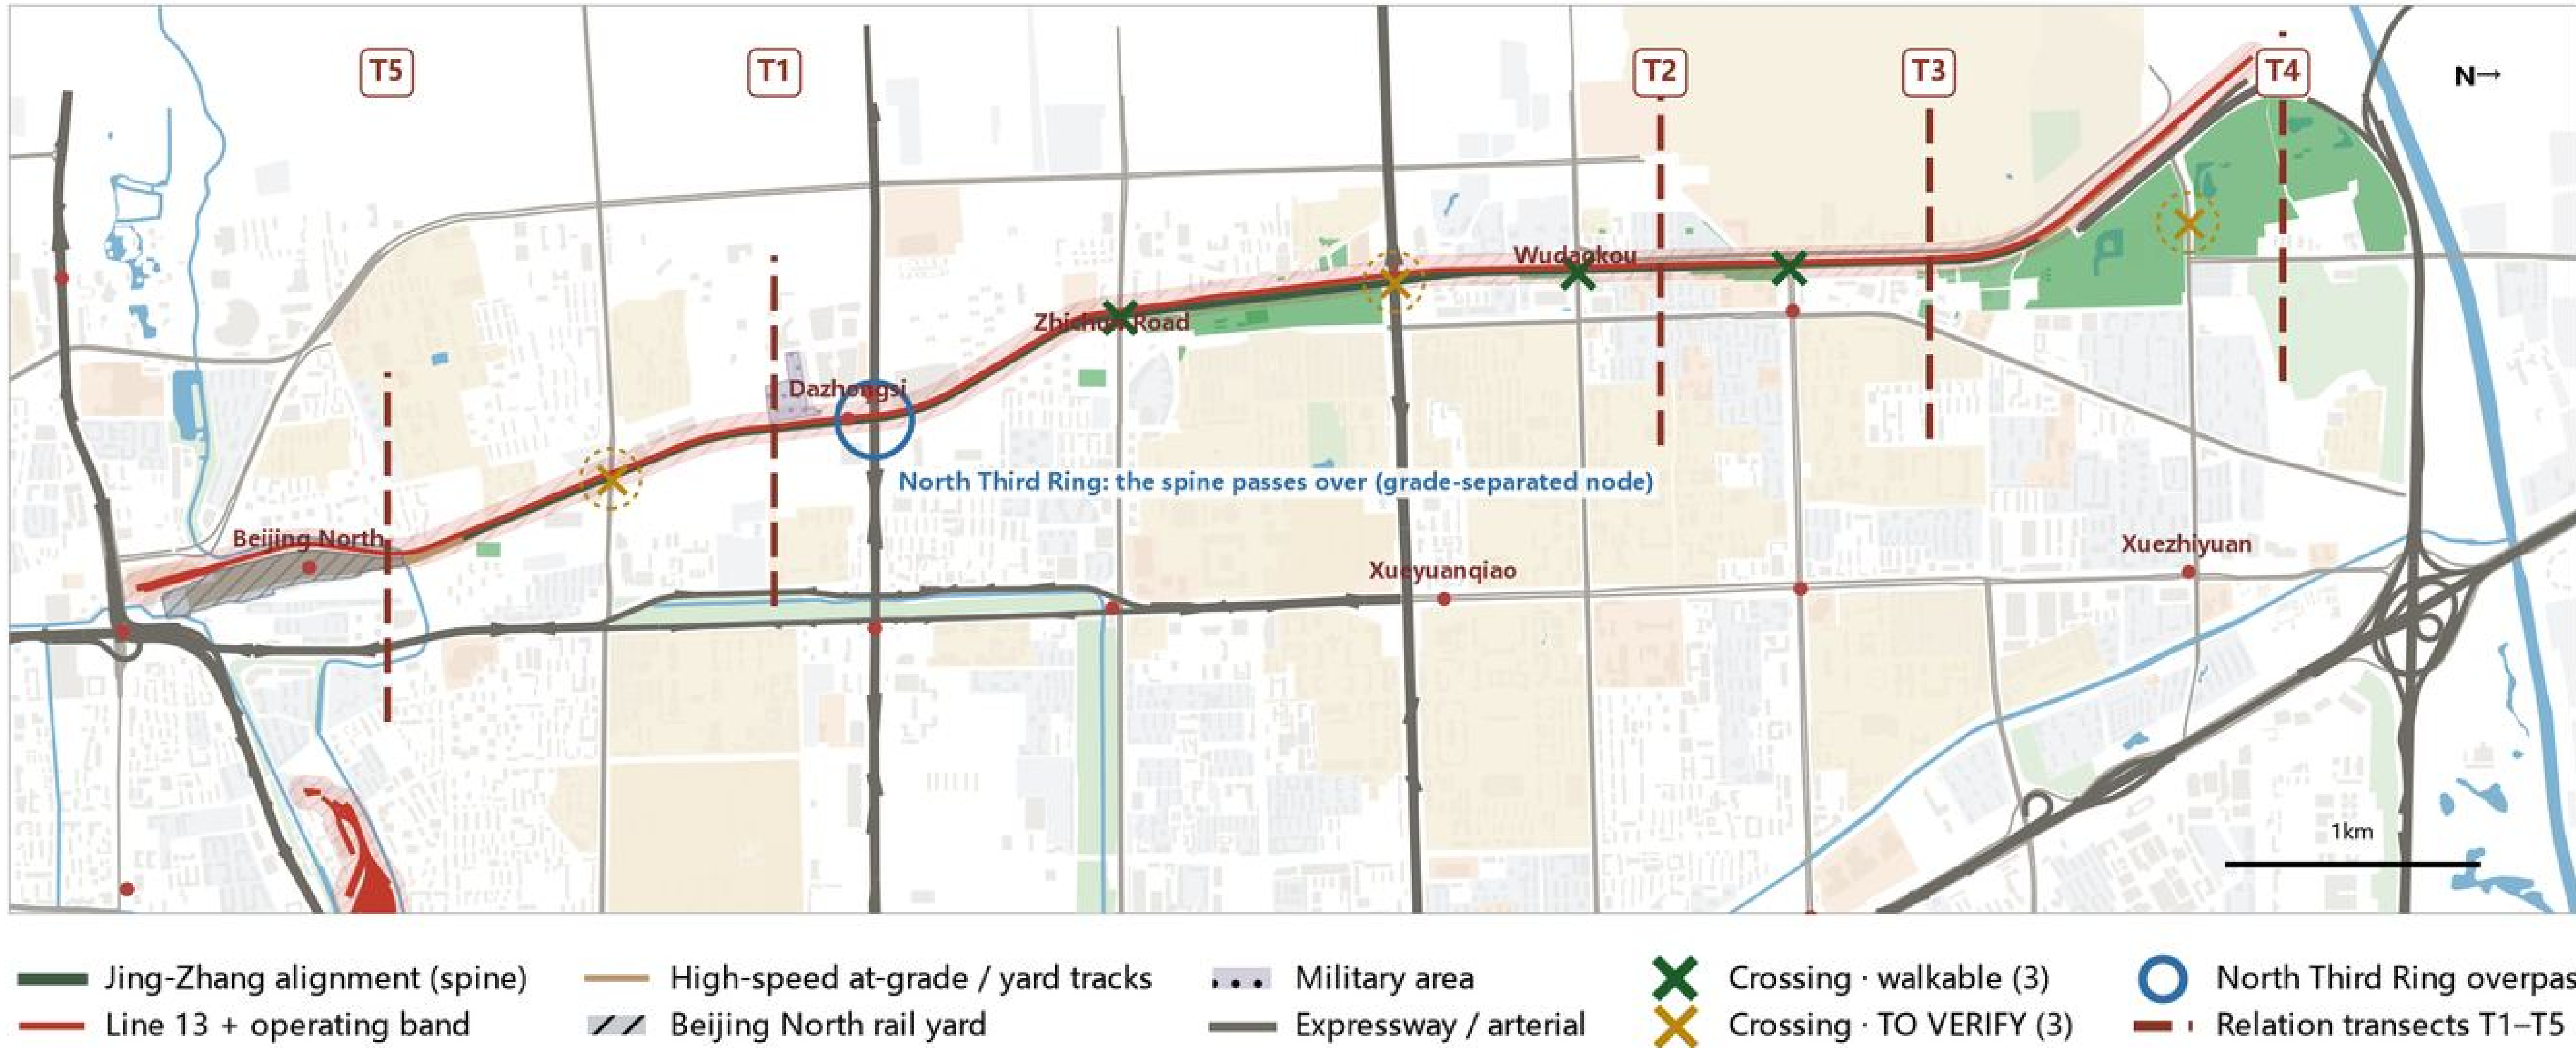


The Line 13 shared corridor, the North Third and Fourth Ring expressways, the Beijing North rail yard and the at-grade high-speed sections form the north–south operating network and, at the same time, the principal east–west barrier; the seven existing crossings fall into three classes by level of verification.


A Station ≠ Real Access | the gap between the 800 m standard catchment and the real walking network

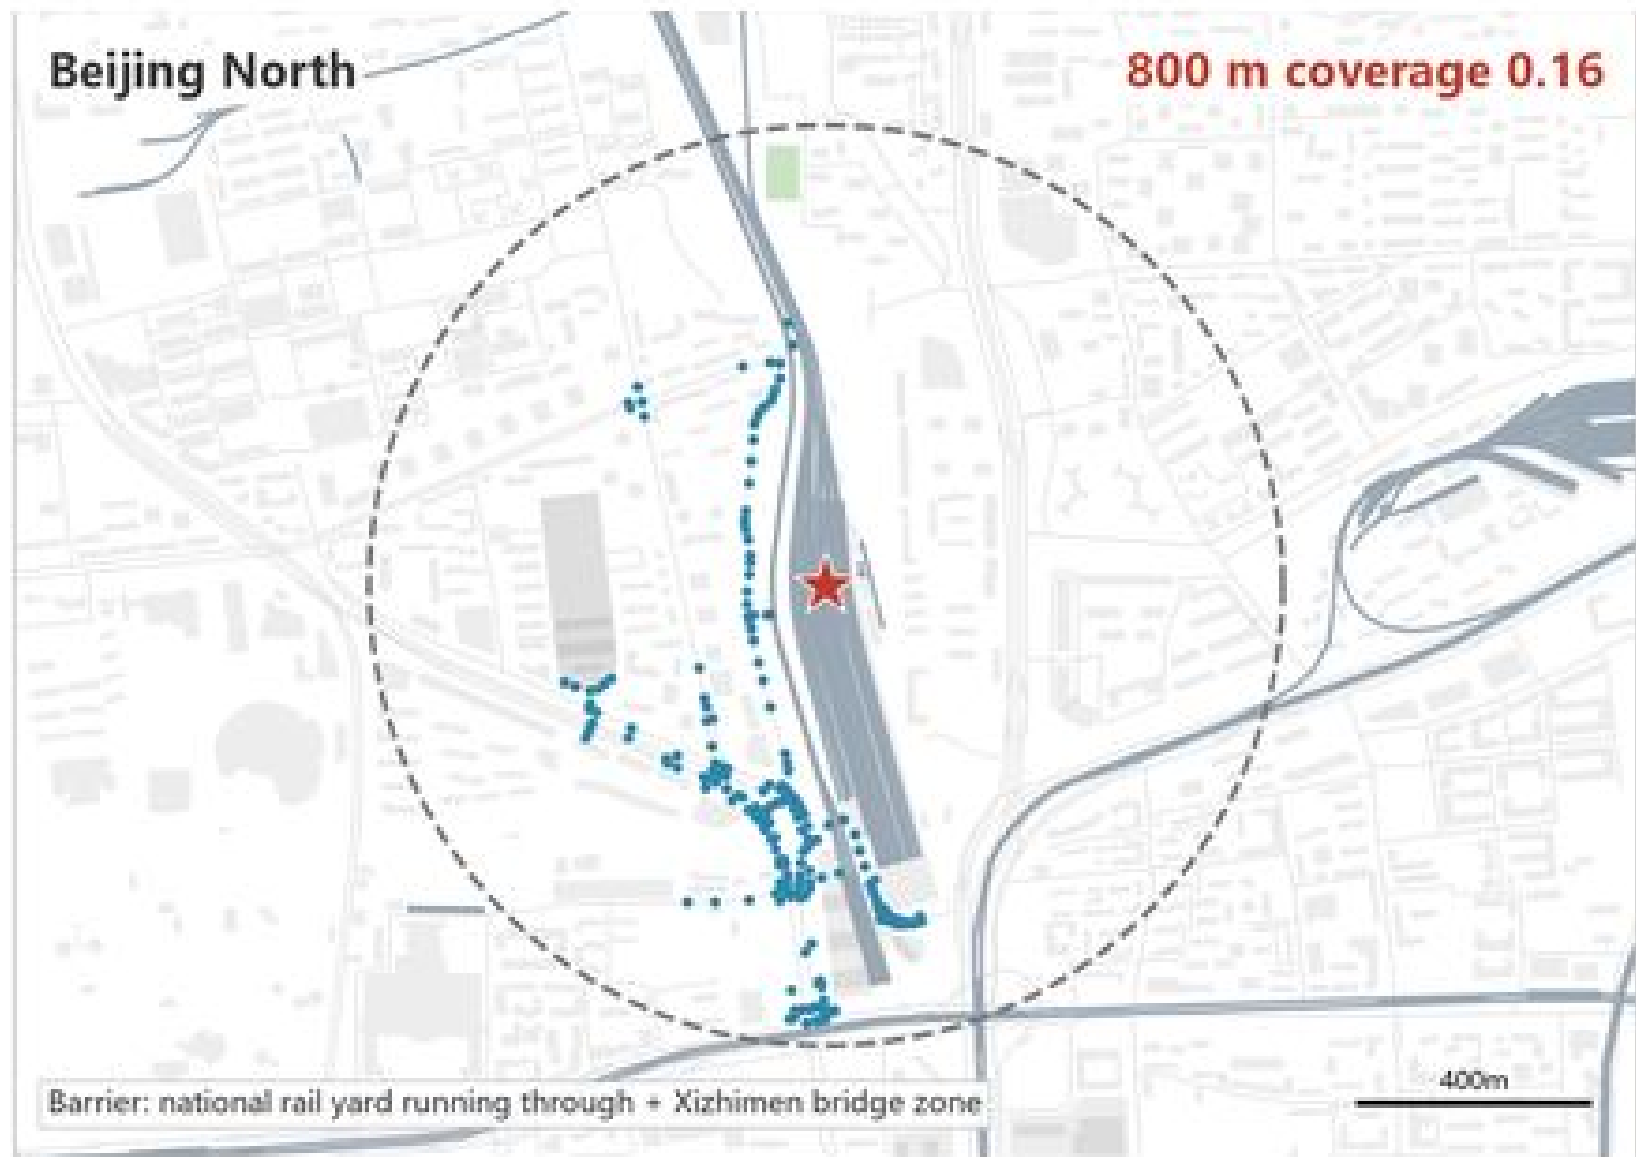


01 Beijing North | coverage 0.16

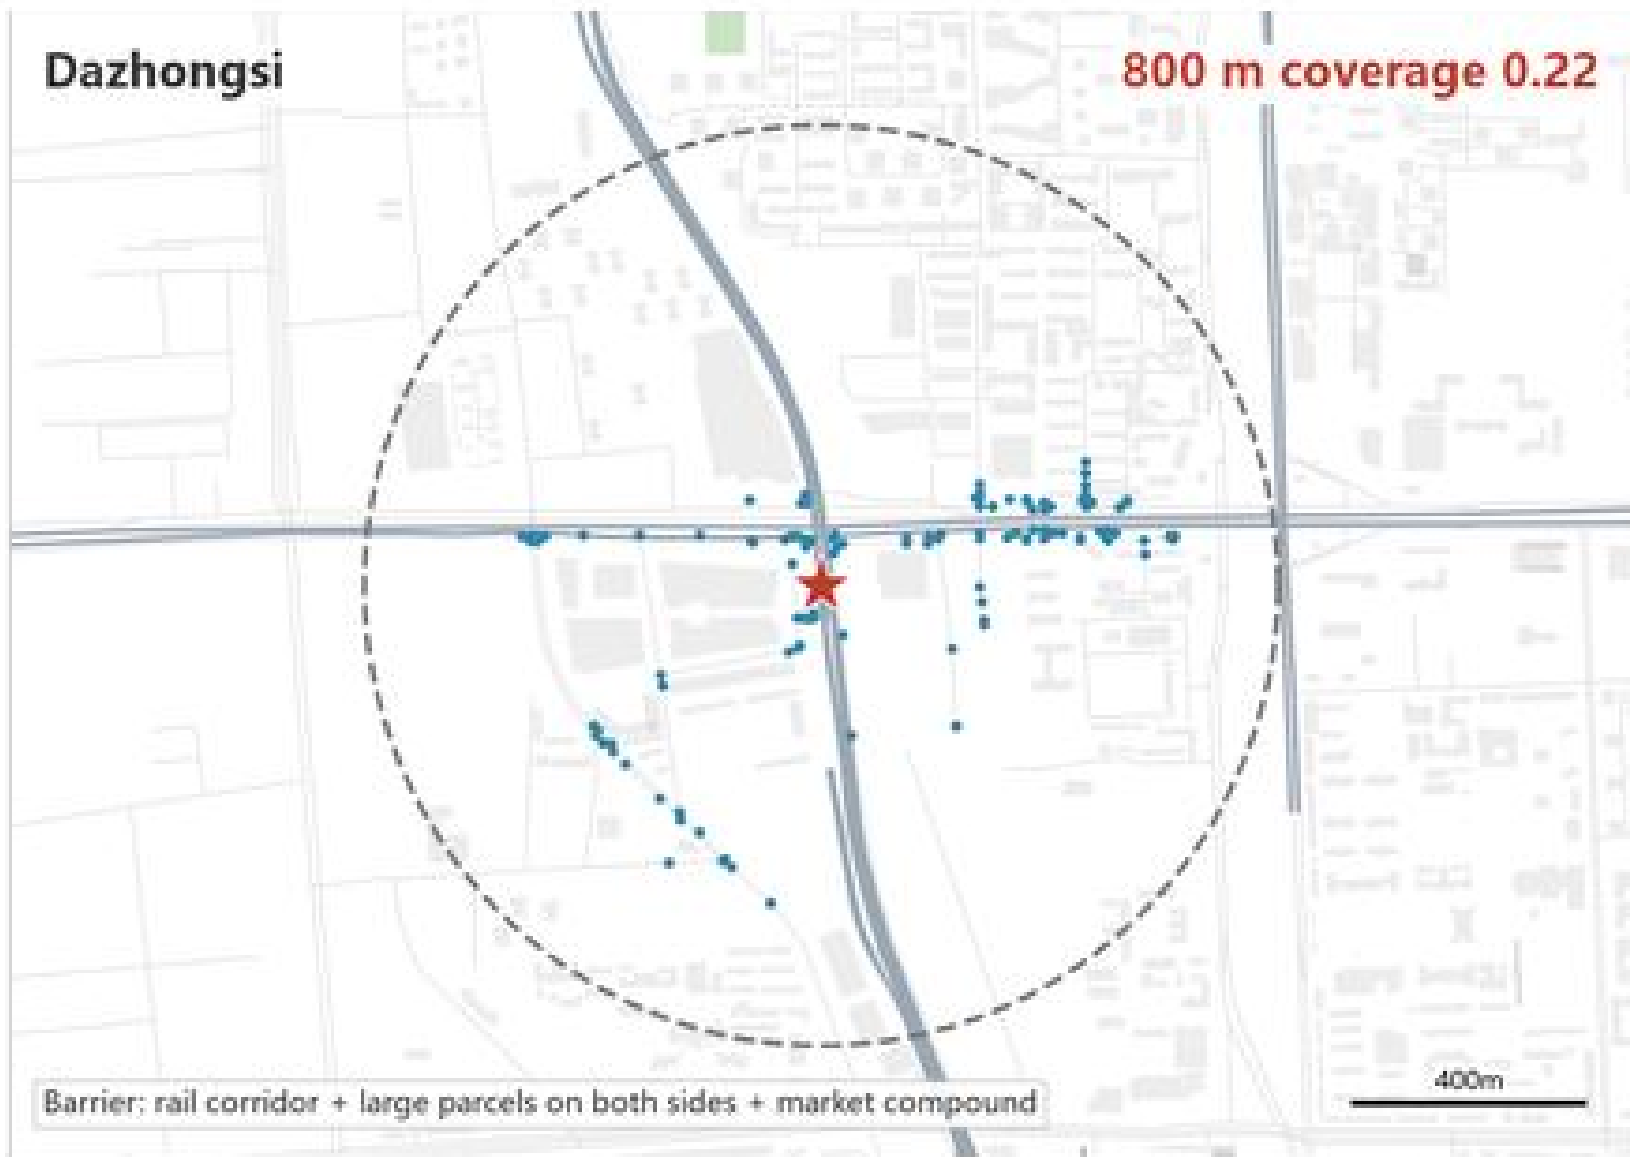


02 Dazhongsi | coverage 0.22

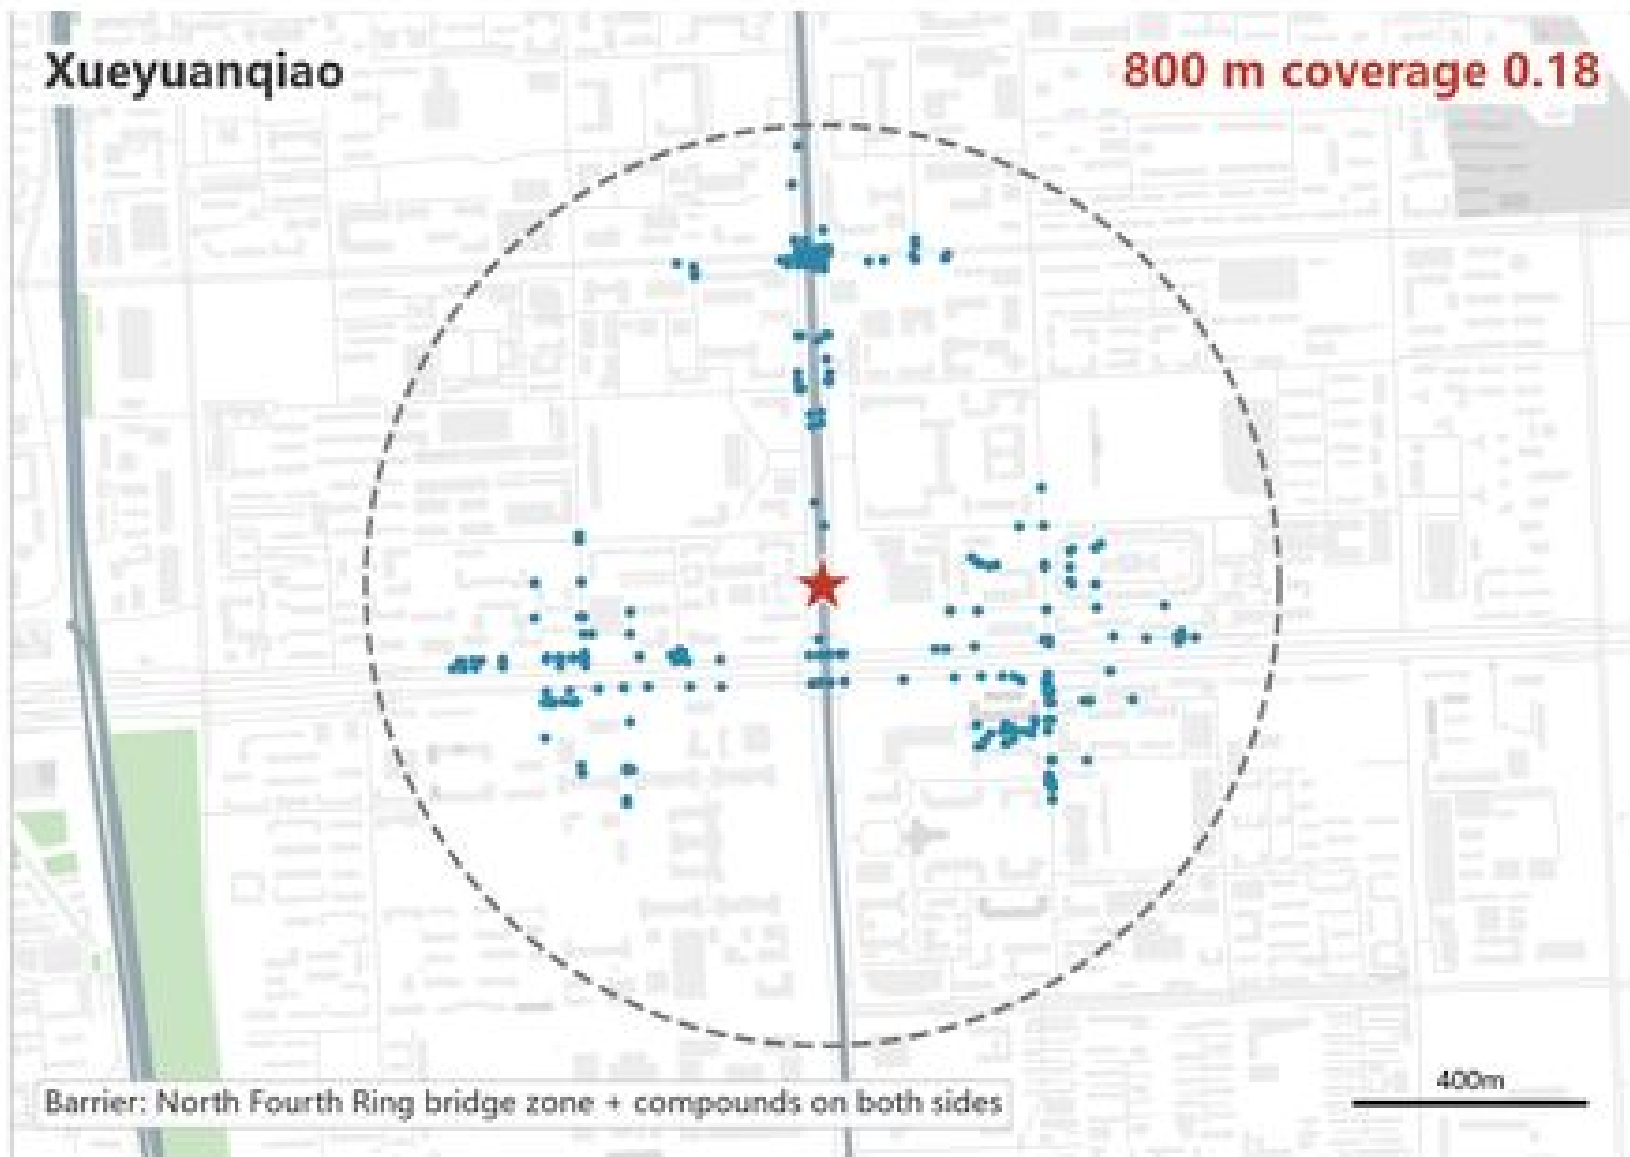

03 Xueyuanqiao | coverage 0.18

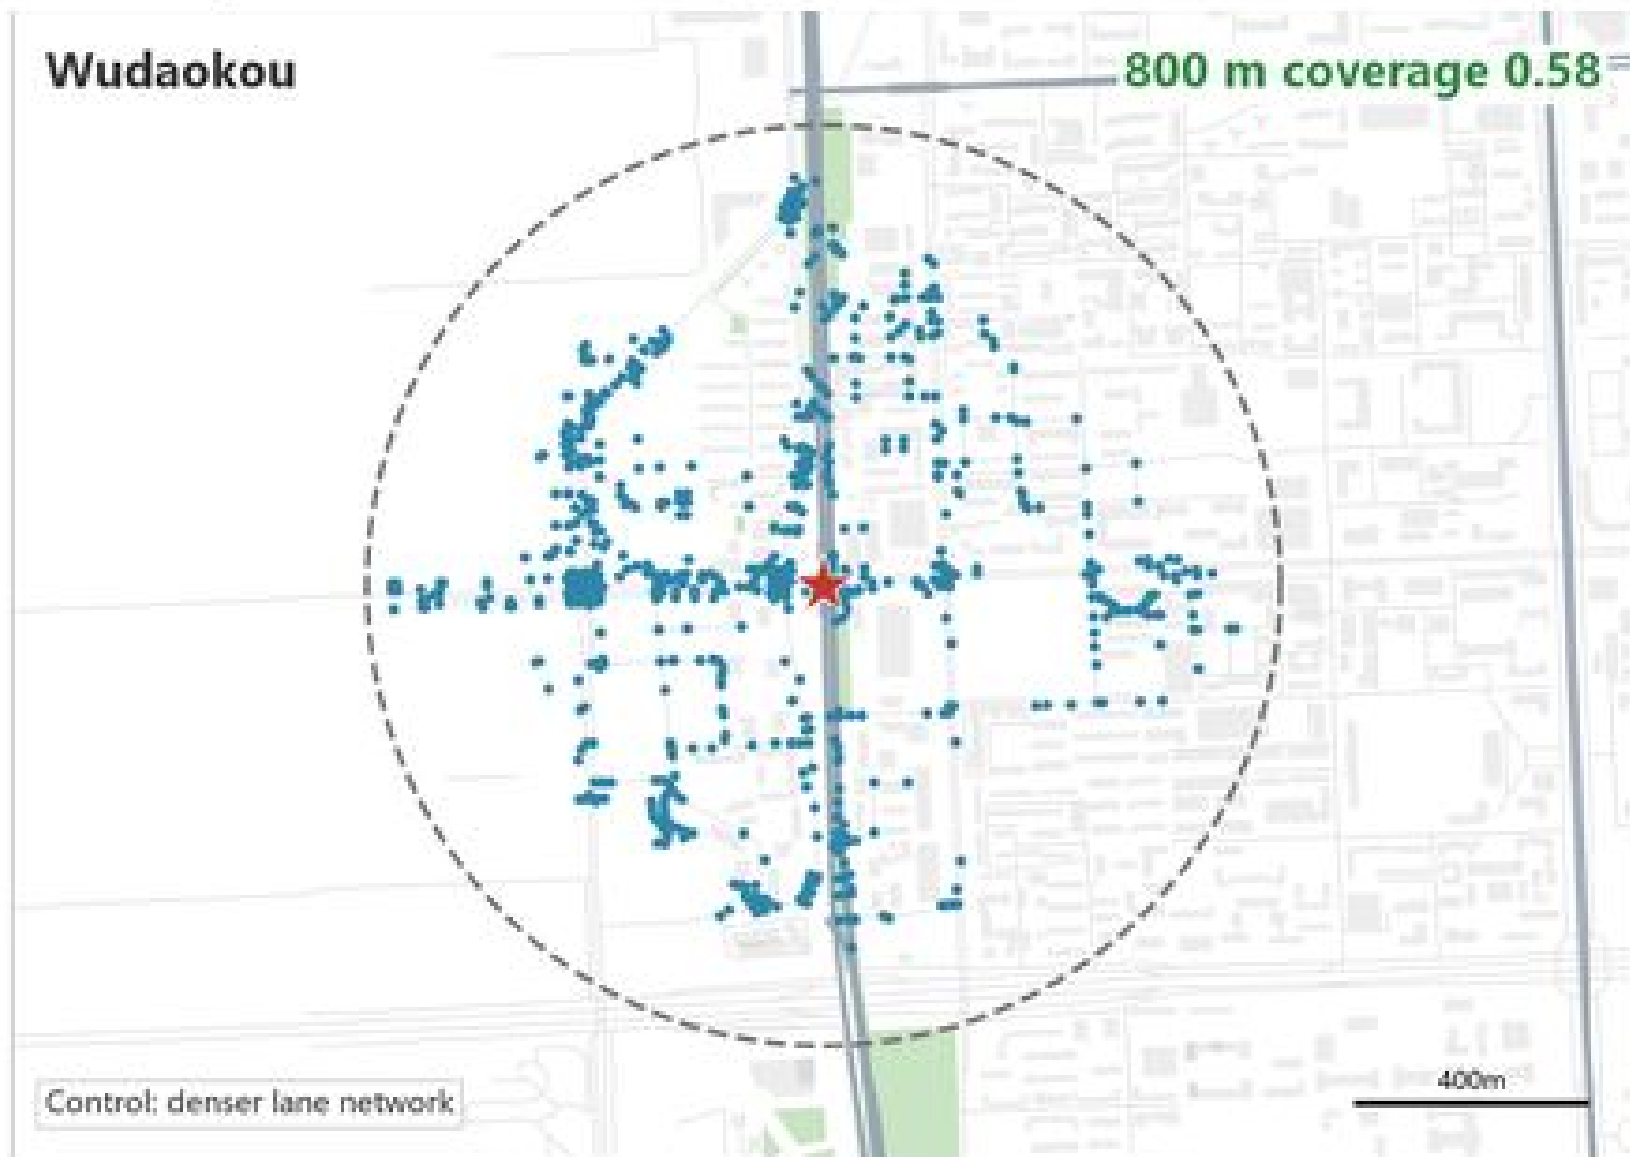

04 Wudaokou | coverage 0.58 (control)

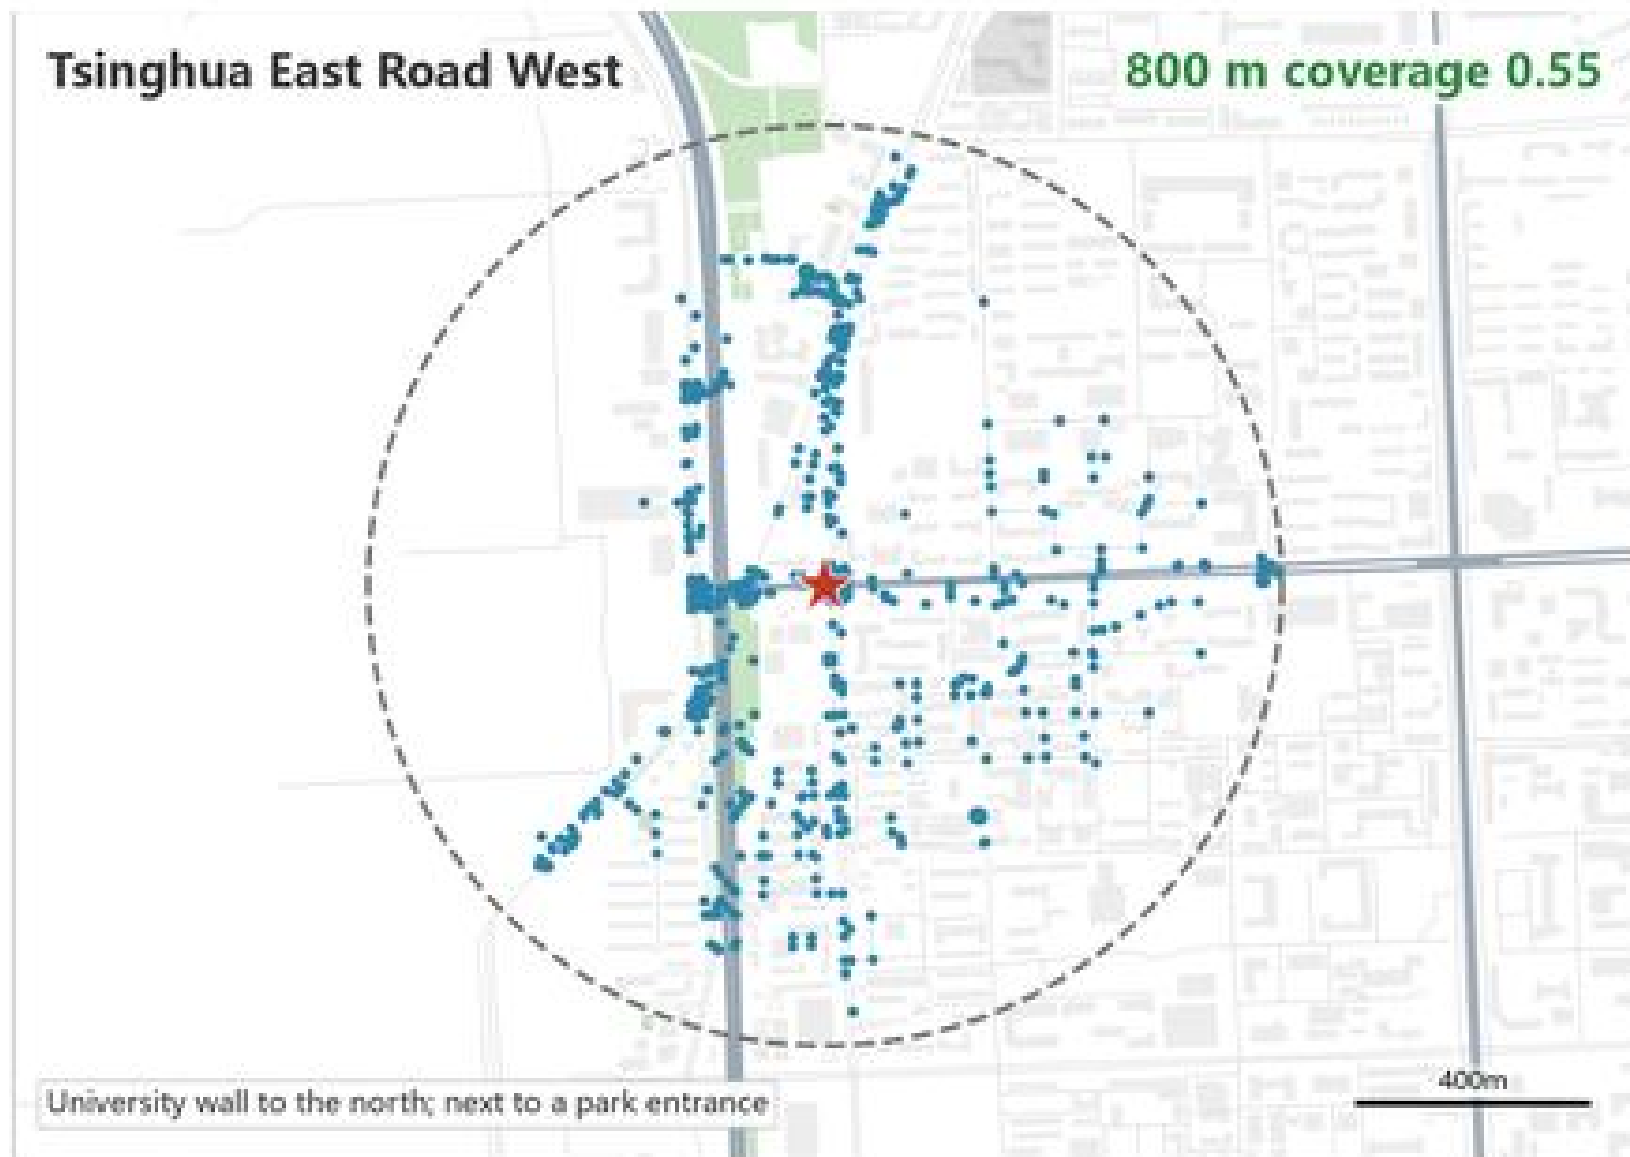

05 Tsinghua East Road West | coverage 0.55 (next to a park gate)

T5 | Railway Terminus → Urban Gateway

Beijing North Railway Station


ARRIVE CROSS




EXISTING URBAN RELATIONS



FUTURE RELATION SCENARIO

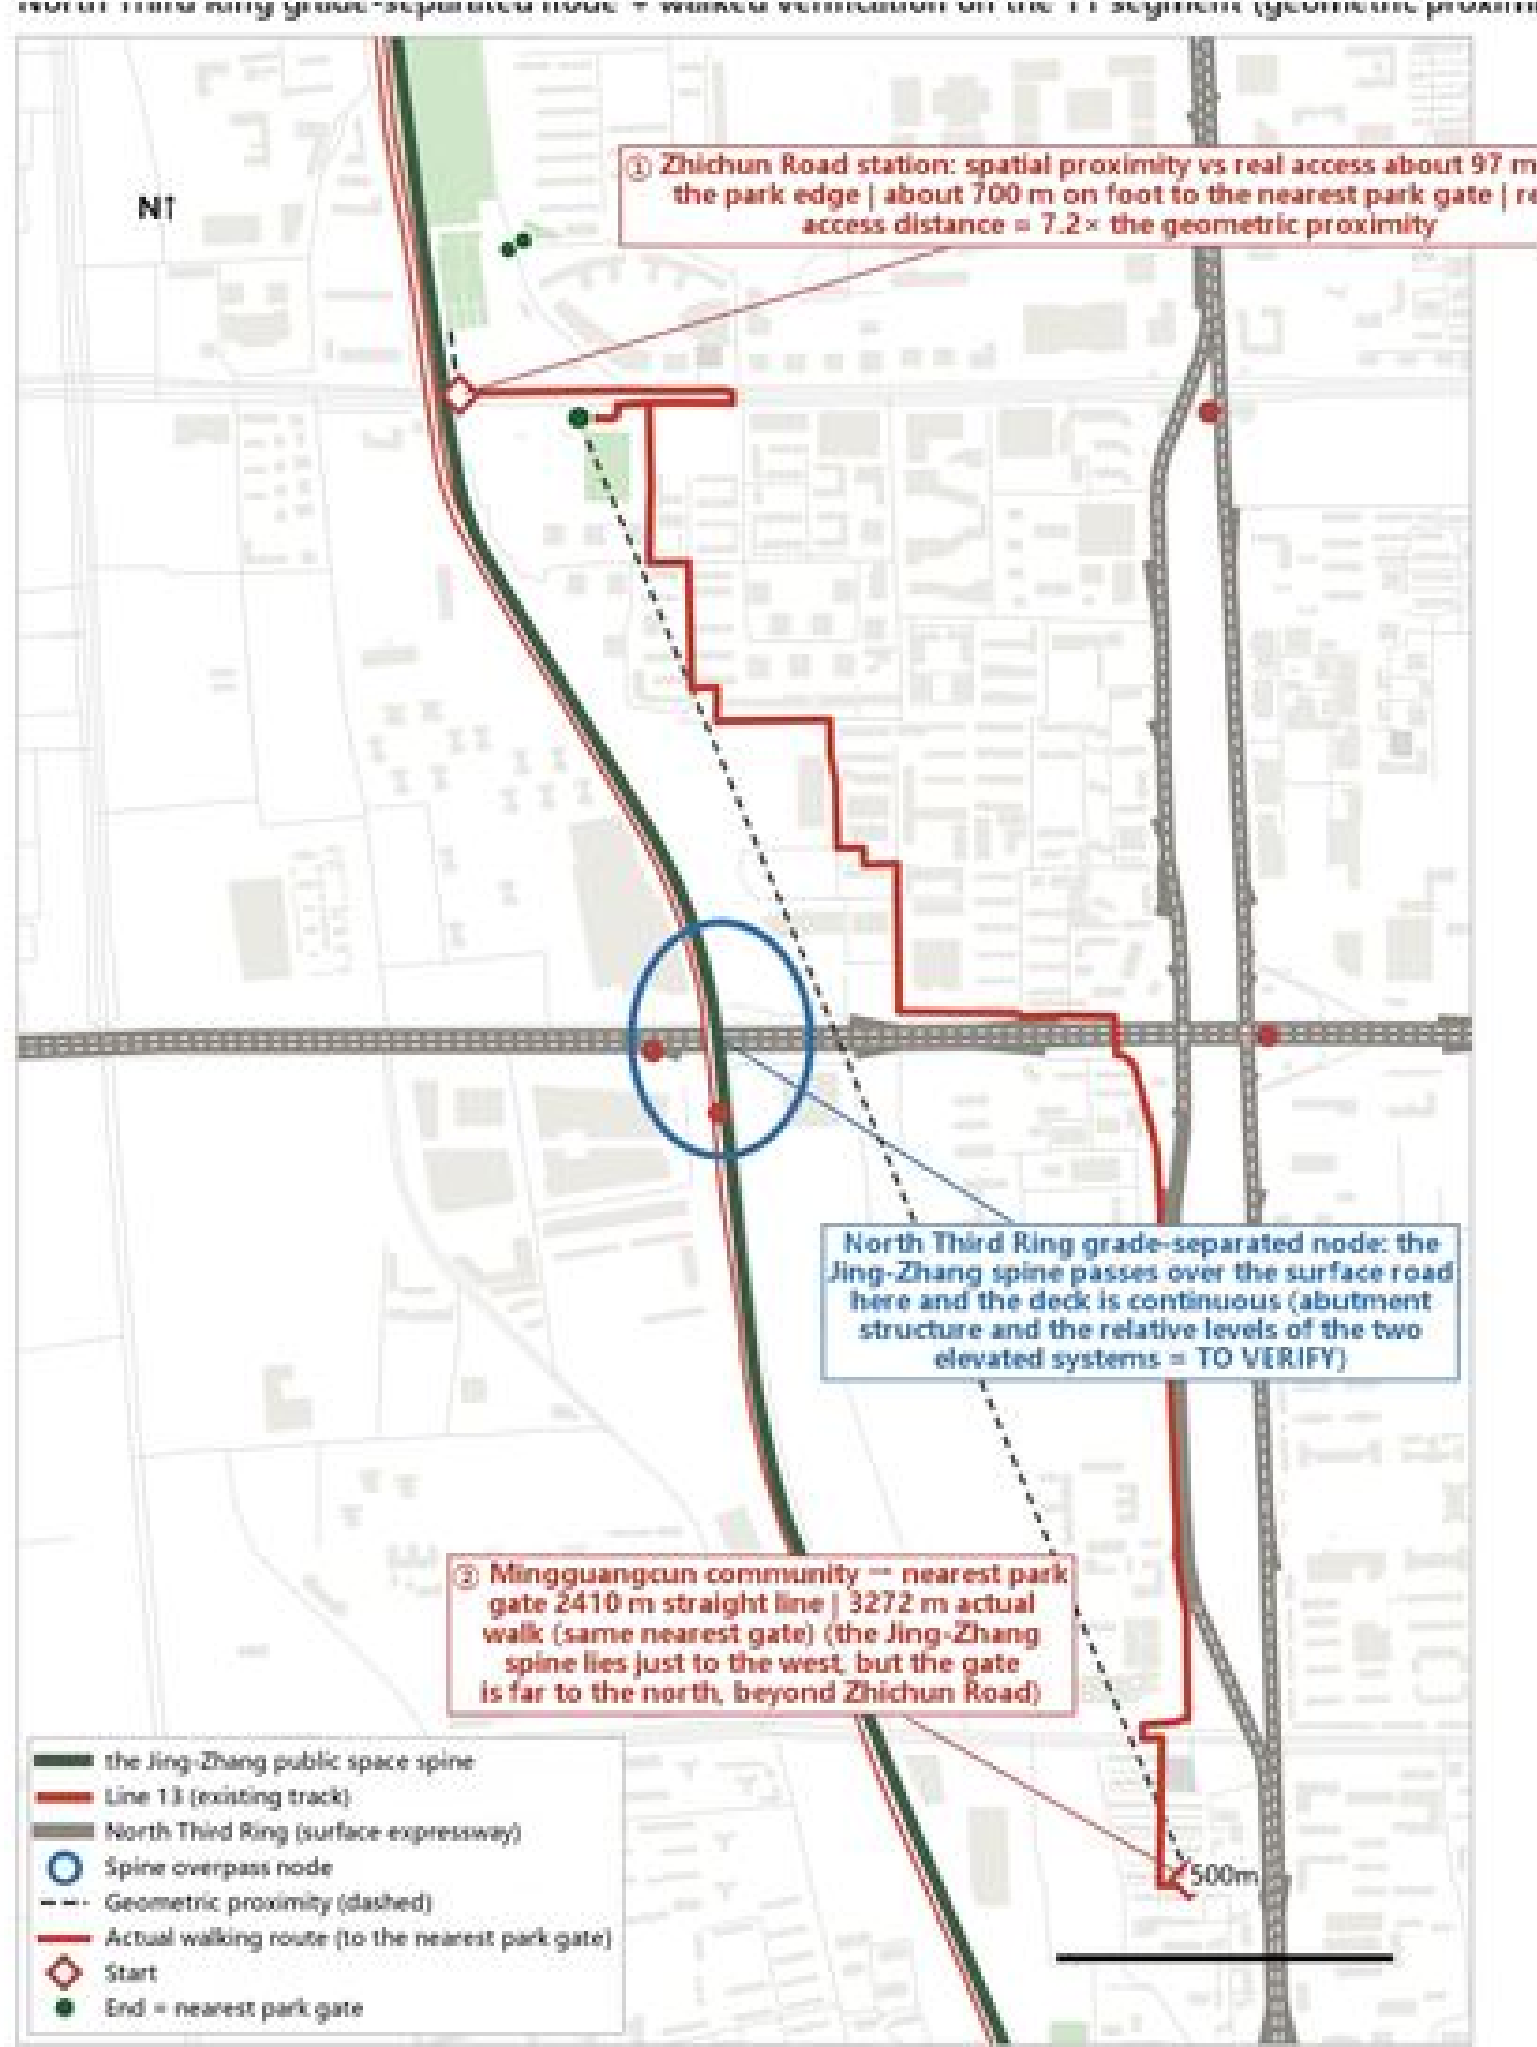

North Third Ring grade-separated node and walked verification on the T1 segment | Zhichun Road station is about 97 m from the park edge but about 700 m on foot from the nearest gate; the Mingguangcun resettlement community is 2,410 m in a straight line and 3,272 m on foot.

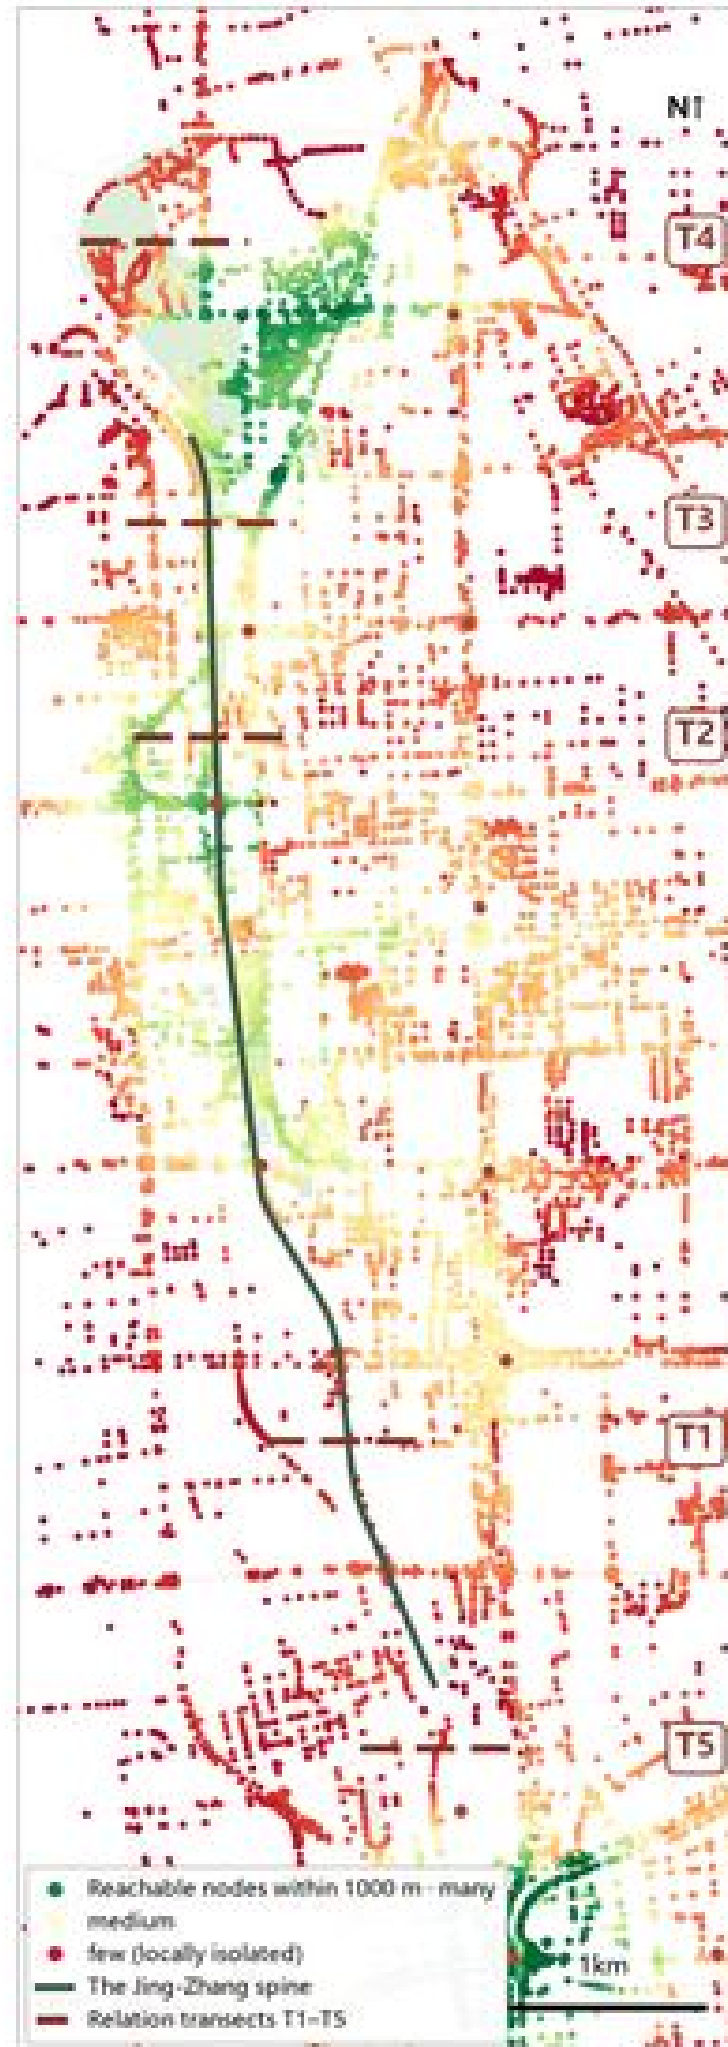

Local connectivity | consistently low around university compounds and rail yards.

It looks close. Why can you not get there?

Crossings exist at only a few points and are mostly purely traffic structures. The gap between spatial proximity and real access is the principal relation problem along this stretch.

Utility support


- Space reserved for environmental sensing
- Continuous path for low-speed devices
- Public information interface

Only conceptual support with present evidence is shown; no pipework, capacity or engineering design is proposed.


Ecological Continuity ≠ Continuous Public Use.

Green space is not background planting but the medium through which industry, everyday life and Jing-Zhang form a public relationship. The point is not more green, but turning the ecological spine into space that can be entered, reached and used.

GREEN system | green spine and structural breaks

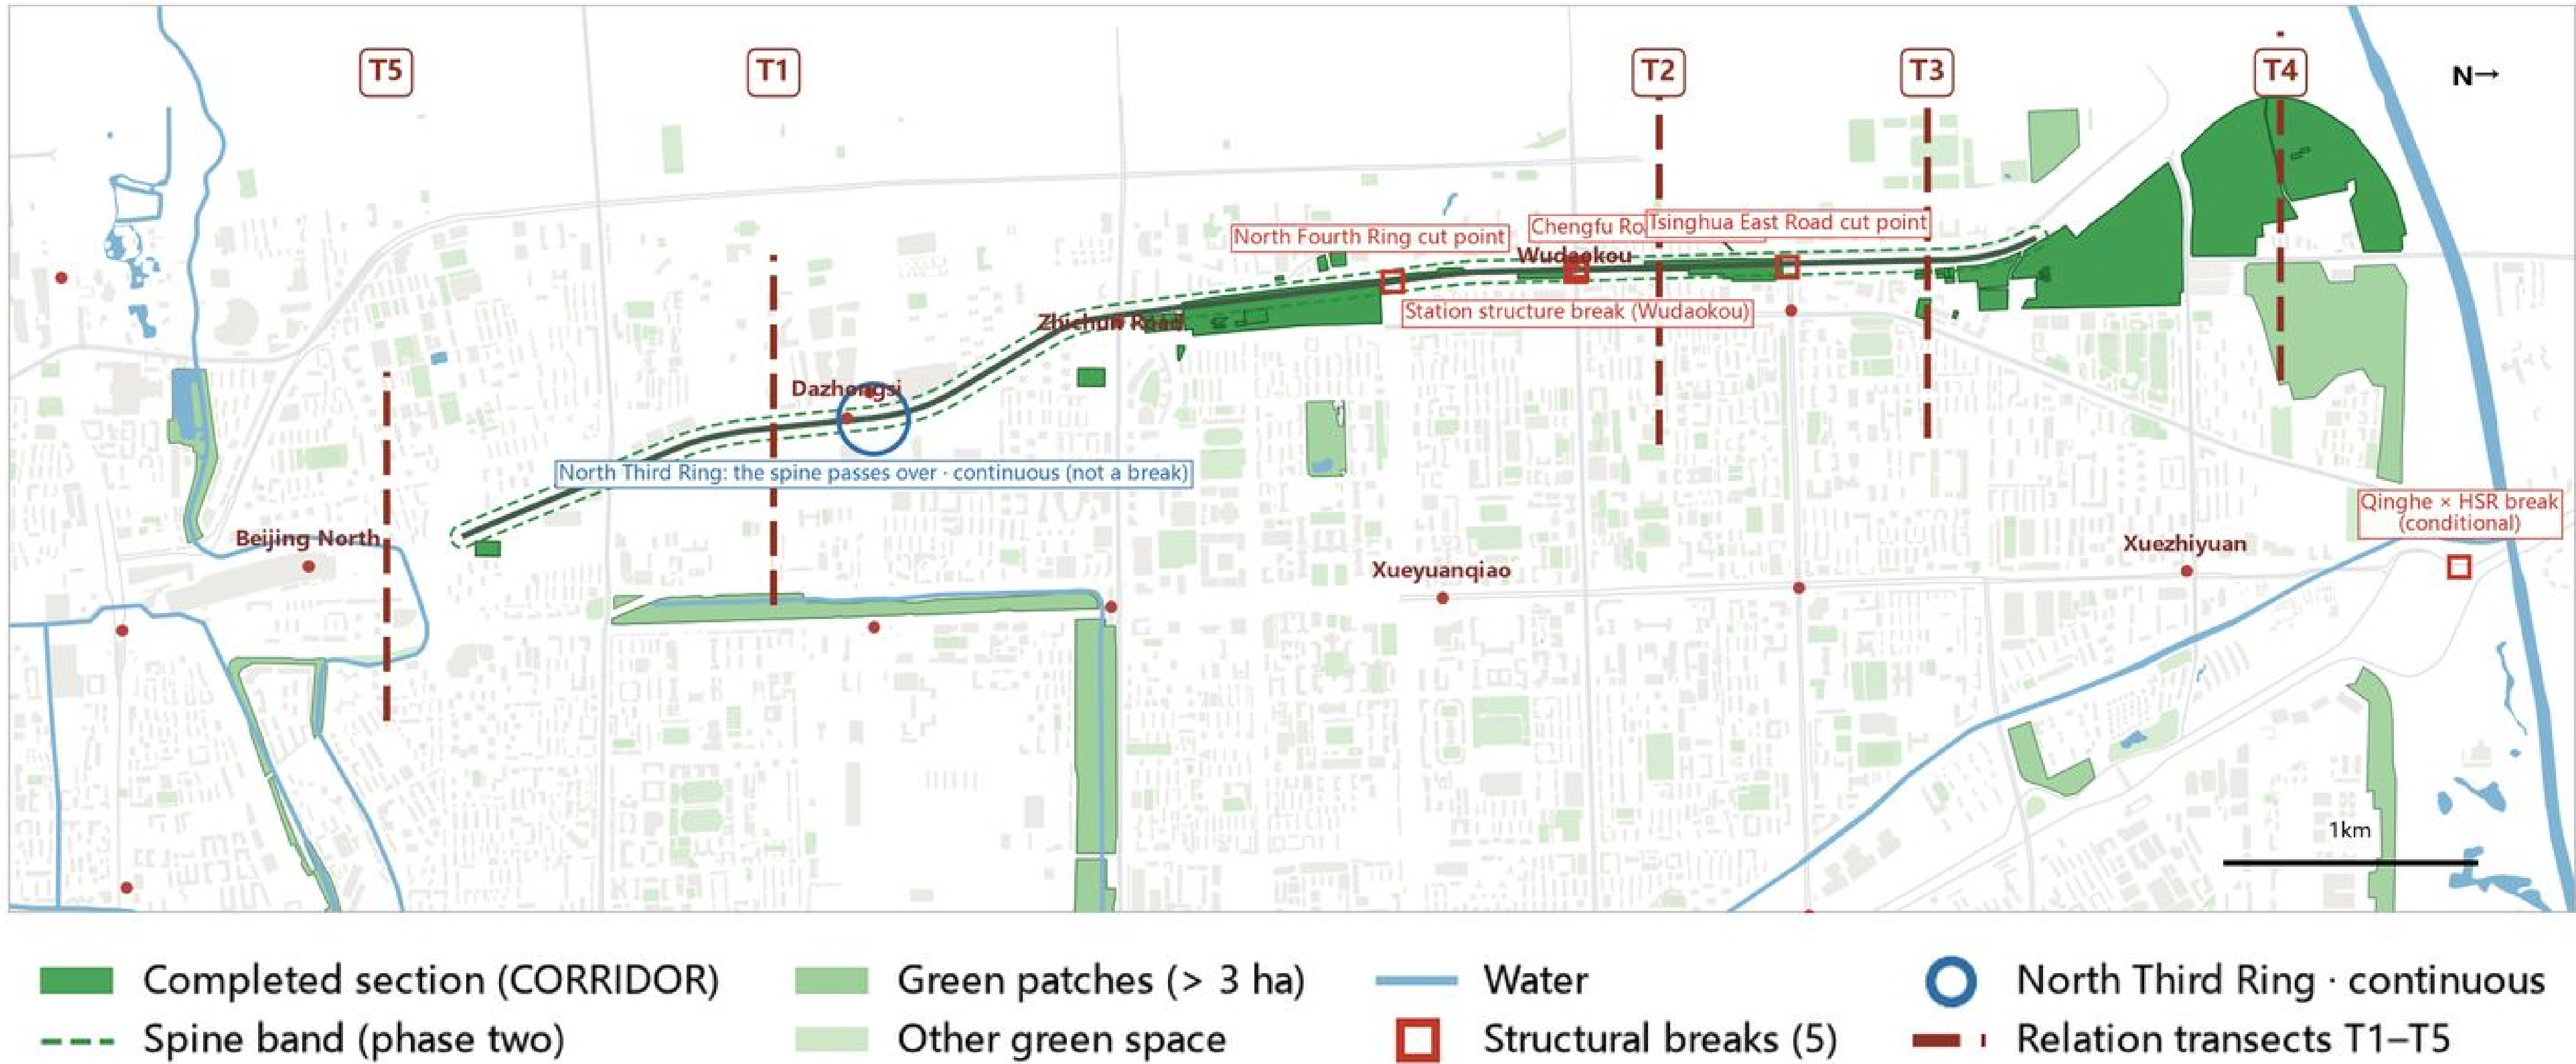

Jing-Zhang is one of the principal continuous green public-space spines within the study area. There are five structural breaks, four of them caused by grey infrastructure; at the North Third Ring the spine passes over and the green corridor stays continuous.

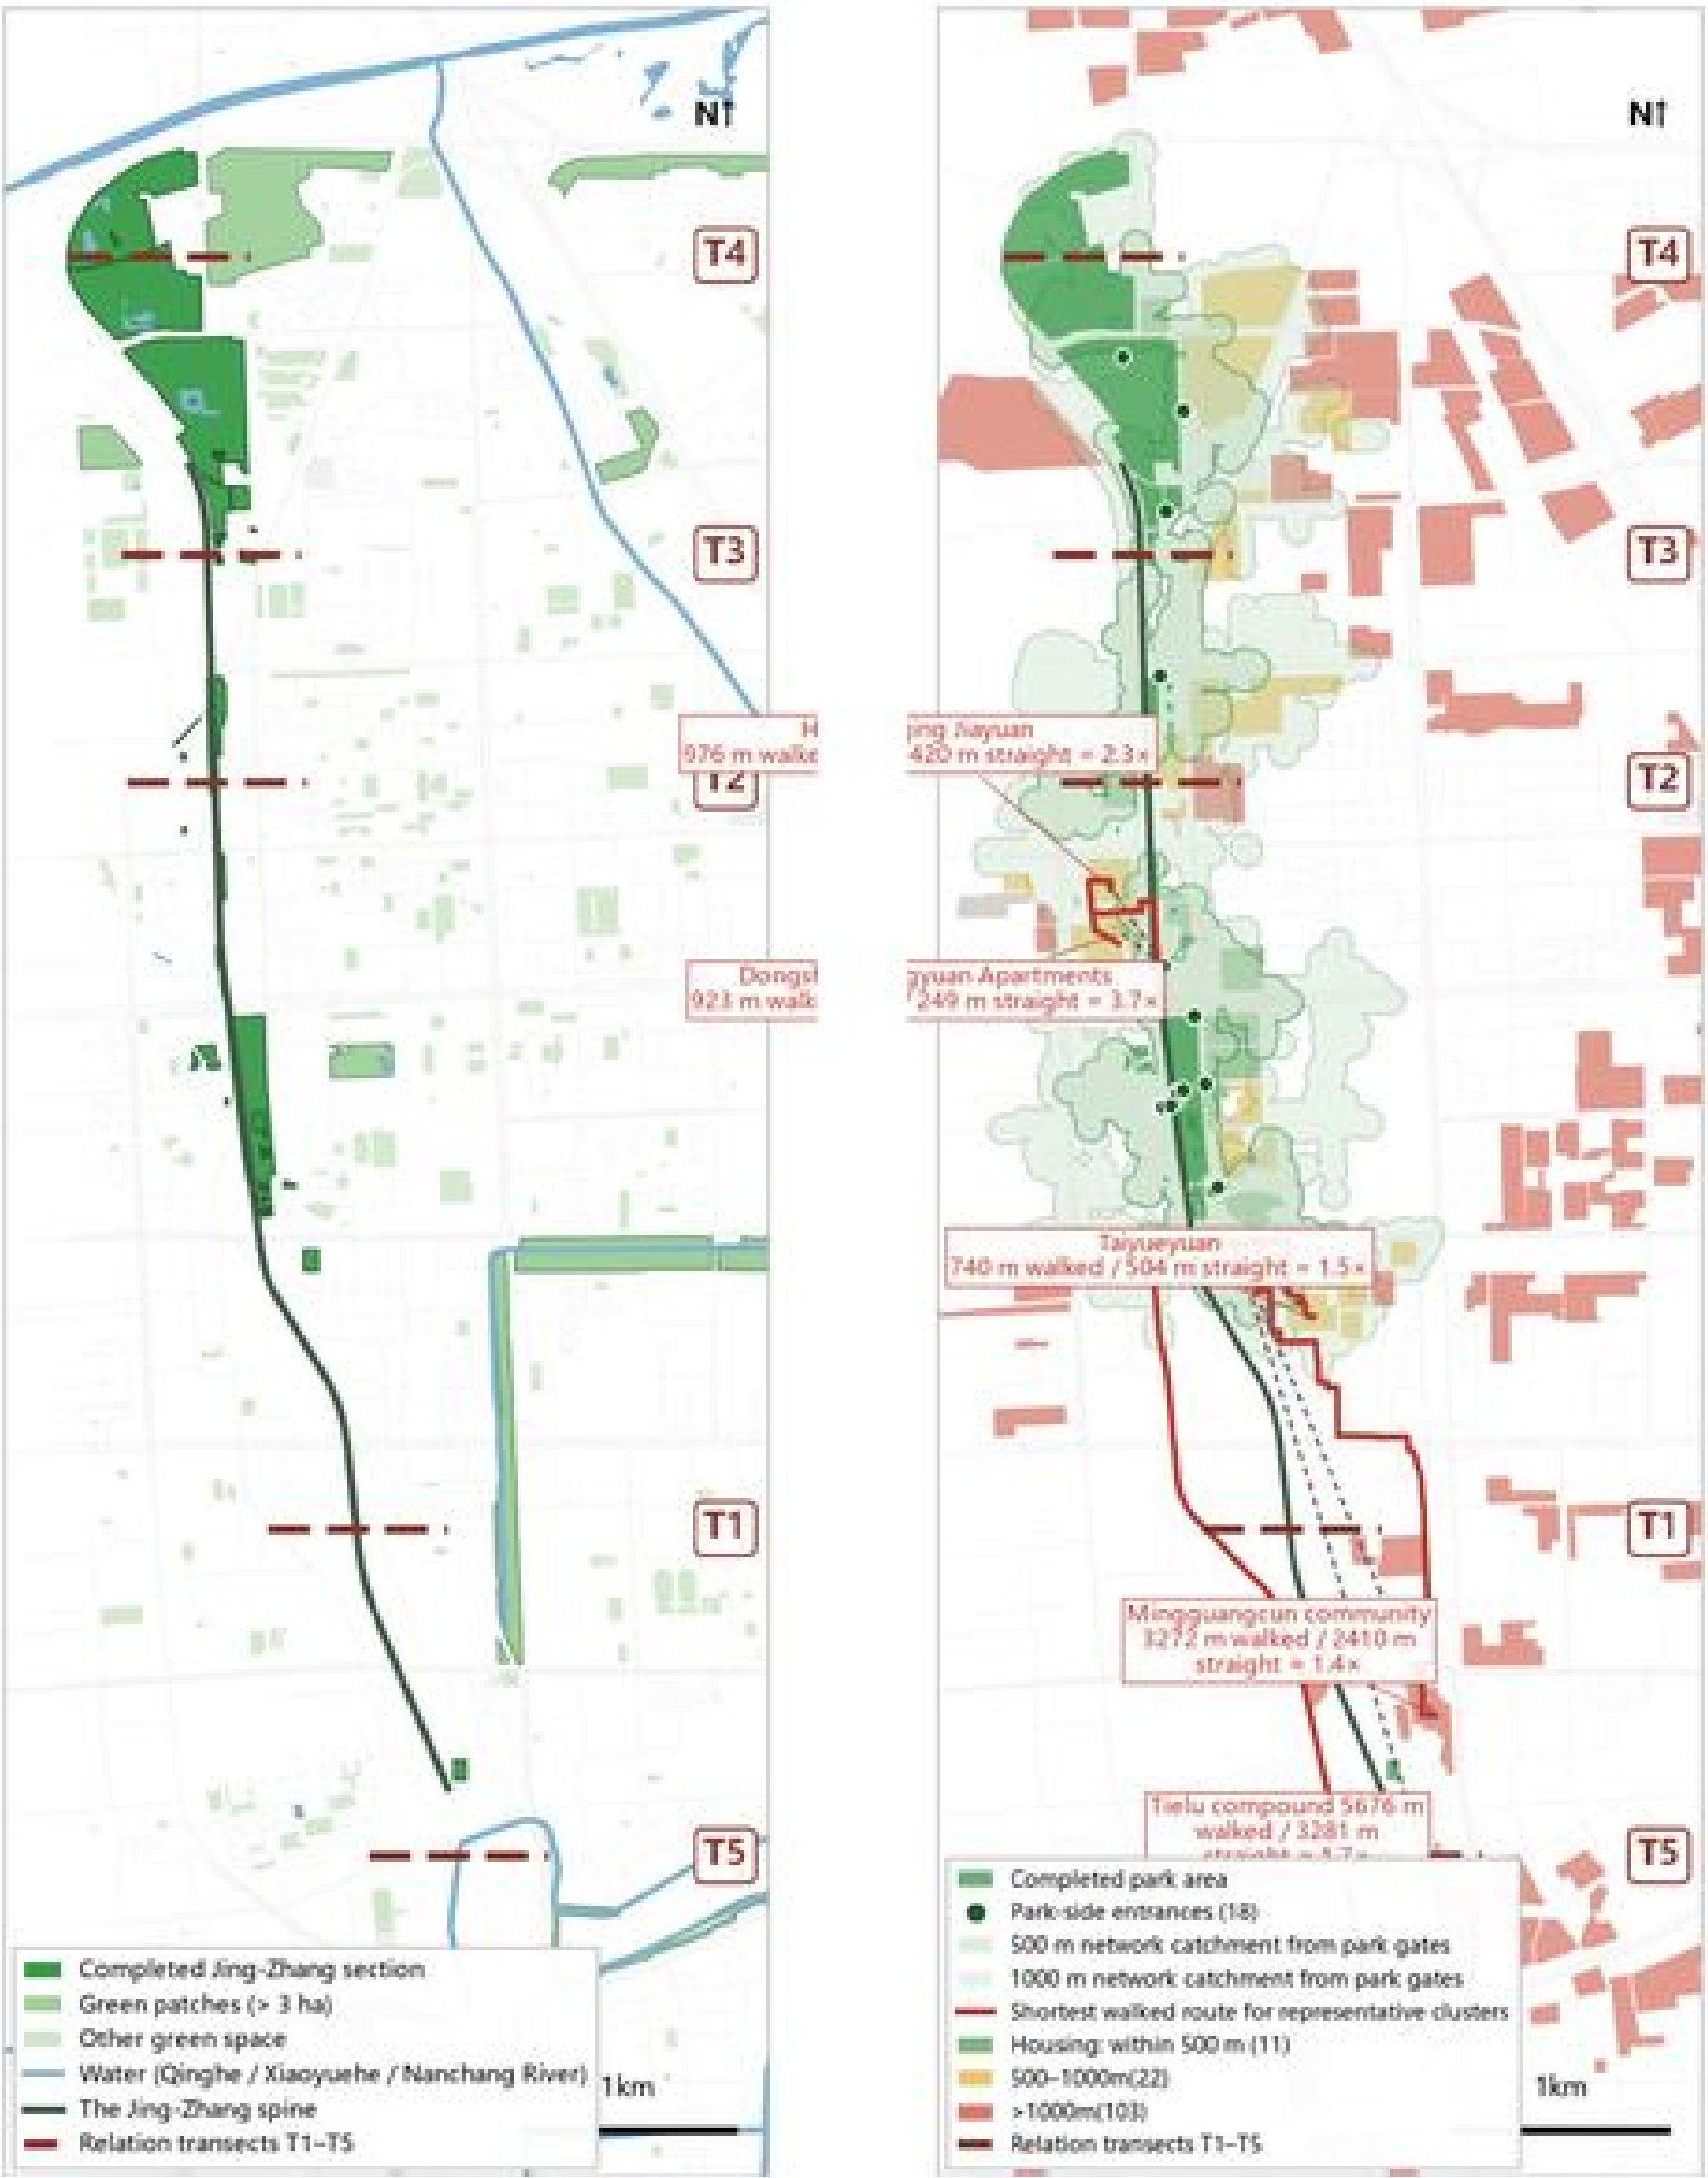

Ecological / physical continuity

Residential areas → real access to Jing-Zhang public space

Green on the Map ≠ Structural Connection

In the northern section green quantity is large and adjacent and the blue line is continuous; the ecological base is not the main problem.

Five structural breaks

Four of them are caused by grey infrastructure.

Adjacent but hard to reach

Large residential areas beyond the rail and the expressway lie more than 1,000 m away.

Entrances decide use

Walked / straight-line ratio 1.4–3.7×; gate location matters more than green quantity.

T4 | Industrial Rear Edge → Urban Frontage

Zhongzhiyuan

FACE

USE



EXISTING URBAN RELATIONS



FUTURE RELATION SCENARIO

Industrial operation → Public ground floor → Semi-outdoor exchange → Public forecourt / everyday green → Jing-Zhang → Urban life

CONDITIONAL GREEN-NETWORK INTERFACE (northern end-Qinghe) is a secondary annotation only: reserved solely if an existing lawful crossing condition holds, and not raised to a primary T4 mechanism.

The three areas carry different tasks and therefore different design depths: only Dazhongsi is taken to object level.

A TASK AREA is the extent the competition asks us to address; a RESPONSE WINDOW is the relationship this proposal actually reorganises within it. They are not the same extent.

A | Dazhongsi AI Industry Cluster


RESPONSE WINDOW T1 Dazhongsi station area | Station–City Relationship Reorganisation

ARRIVEFACECROSS

OBJECT-LEVEL DESIGN



KEY DESIGN SECTION | GROUND-LEVEL ARRIVAL → TWO-LEVEL PUBLIC HINGE WITHIN THE STATION → UPPER-LEVEL PUBLIC TRANSFER → LINE 13 PLATFORM + JING-ZHANG RAILWAY HERITAGE PARK.

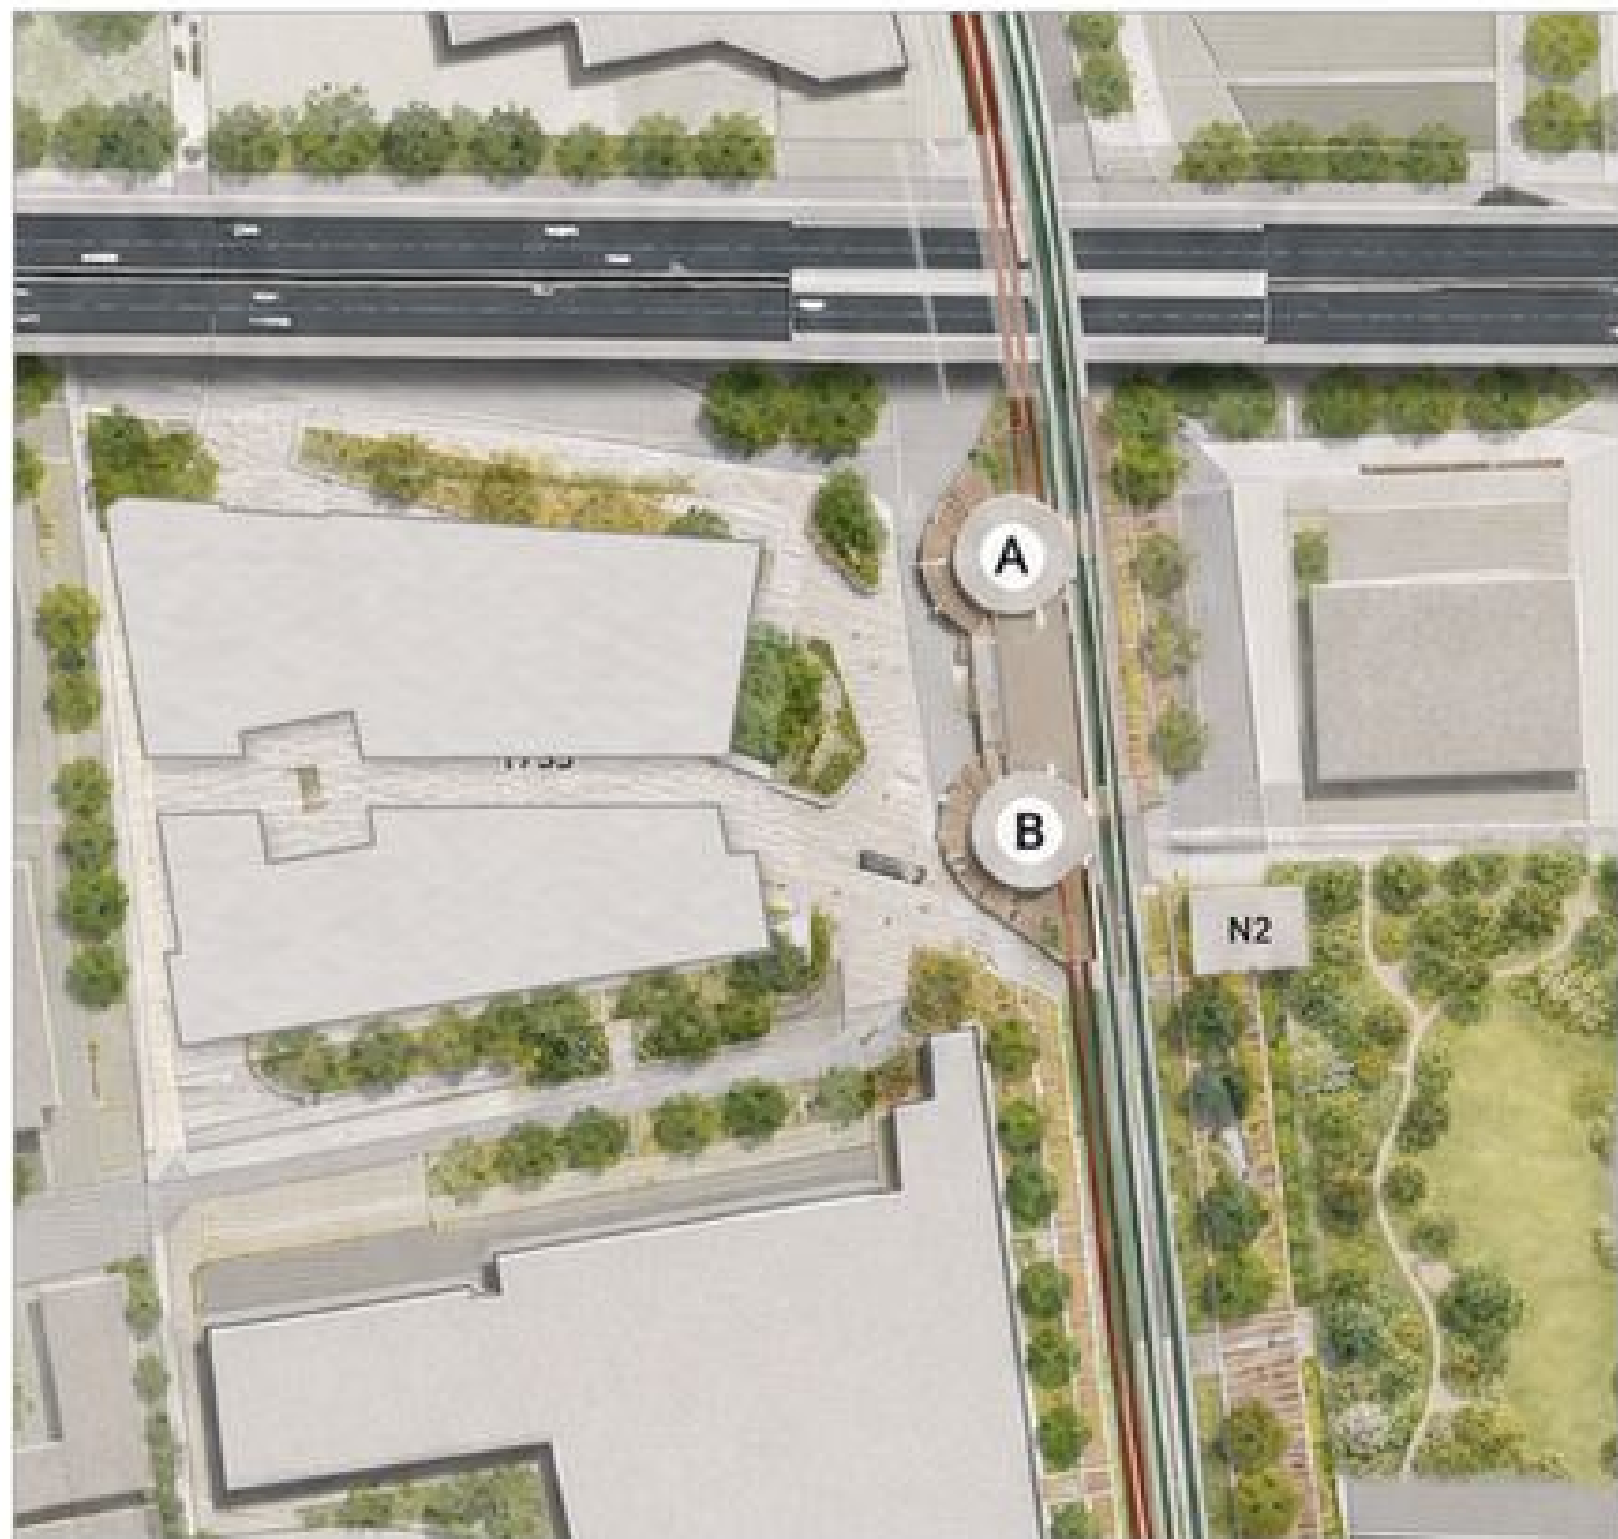

CORE NODE PARTIAL PLAN



CORE NODE AERIAL VIEW

Core design moves

01 OPEN

City approach → the 1733 forecourt → Entrance A / Entrance B

02 HINGE

A two-level public transfer hinge within the station; no change to rail engineering

03 RELEASE

Released towards the Jing-Zhang spine, N2, the eastern public space and the city on both sides

VERIFIED: plan-level factual relations between 1733, Entrances A/B, the station structure, Line 13, Jing-Zhang and the North Third Ring.

TO VERIFY: exact levels, vertical circulation within the station structure, engineering interfaces, landing conditions of N2.

NOT PROPOSED AT THIS STAGE: any unverified new rail crossing.

Official task objects | location key




Task-area extents are indicative (provisional), not official redlines; areas are the published figures.

B | Beijing AI Origin Community

About 104.3 ha | world-class AI innovation ecosystem

RESPONSE WINDOW T2 (adjacent condition: the T3 campus boundary)

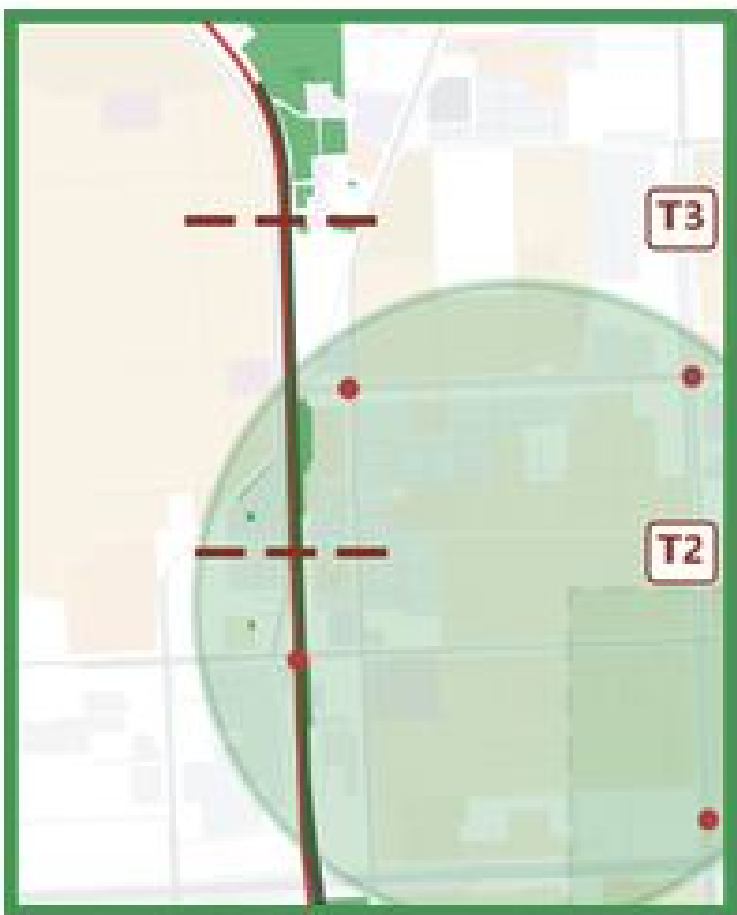


- 01 Near-campus innovation translation network
- 02 Station exchange node
- 03 Campus boundary gradient
- 04 Everyday living base for talent
- 05 Low-disturbance incremental renewal

STRATEGIC FRAMEWORK + CONCEPTUAL SPATIAL CONTROL FOR THE T2/T3 RESPONSE WINDOW

C | Zhongzhiyuan AI Autonomous Innovation Acceleration Area

About 192.1 ha | full-stack autonomous AI innovation system

RESPONSE WINDOW T4

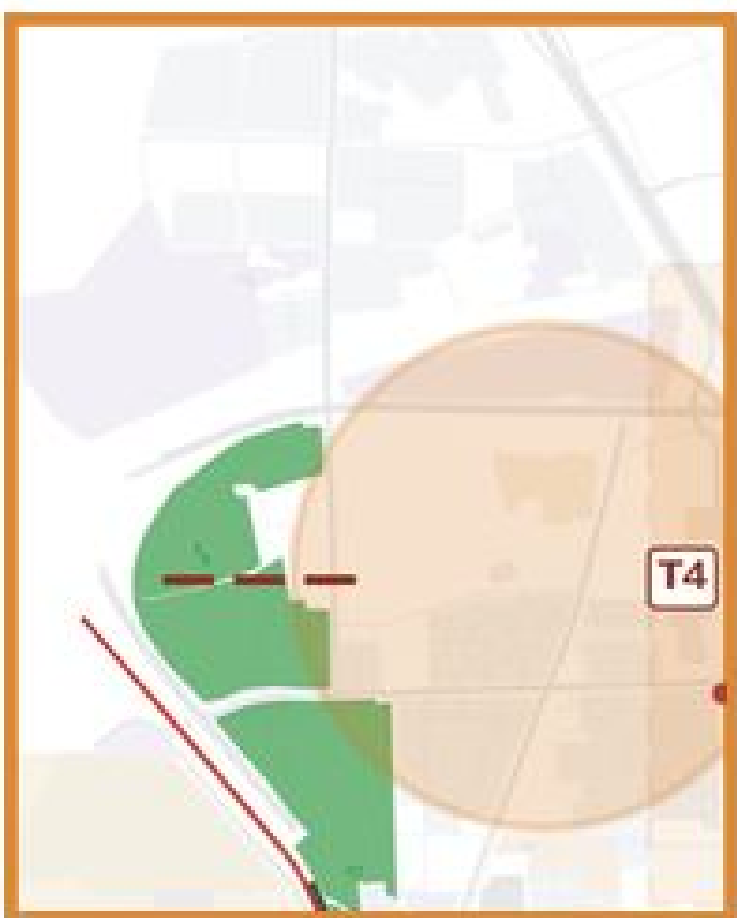

- 01 Full-stack AI industrial base
- 02 Public innovation interface
- 03 Integration of buildings, green space and water
- 04 Industry display and public exchange network
- 05 External transport and green interfaces

STRATEGIC FRAMEWORK + CONCEPTUAL SPATIAL CONTROL FOR THE T4 RESPONSE WINDOW

Why the three areas differ in design depth

Dazhongsi is the only place along the corridor where several problem types overlap in the same segment and where the factual record is most complete; it is therefore taken to object level, with a partial plan and a key section. The other two areas are answered with a strategic framework plus conceptual spatial control at the response window: no precise parcel placement, no building scale, no retain/renovate/demolish judgement and no statutory land-use change.


Delivery is not an investment schedule, but a question of which mode applies to which segment.

Twelve scenario cards (three of them industry test-and-verification scenarios), three landmarks upgraded from existing urban relation nodes, four delivery modes and a three-phase sequence, all on the same spine and the same set of positions.

Corridor-wide scenario — space — operation network

Corridor-wide scenarios and single entry point

S08 Heritage interpretation (nodes along the corridor) S10 Environmental-sensing verification in public space (pilot segment) Scenario opening catalogue | single entry point and application rules

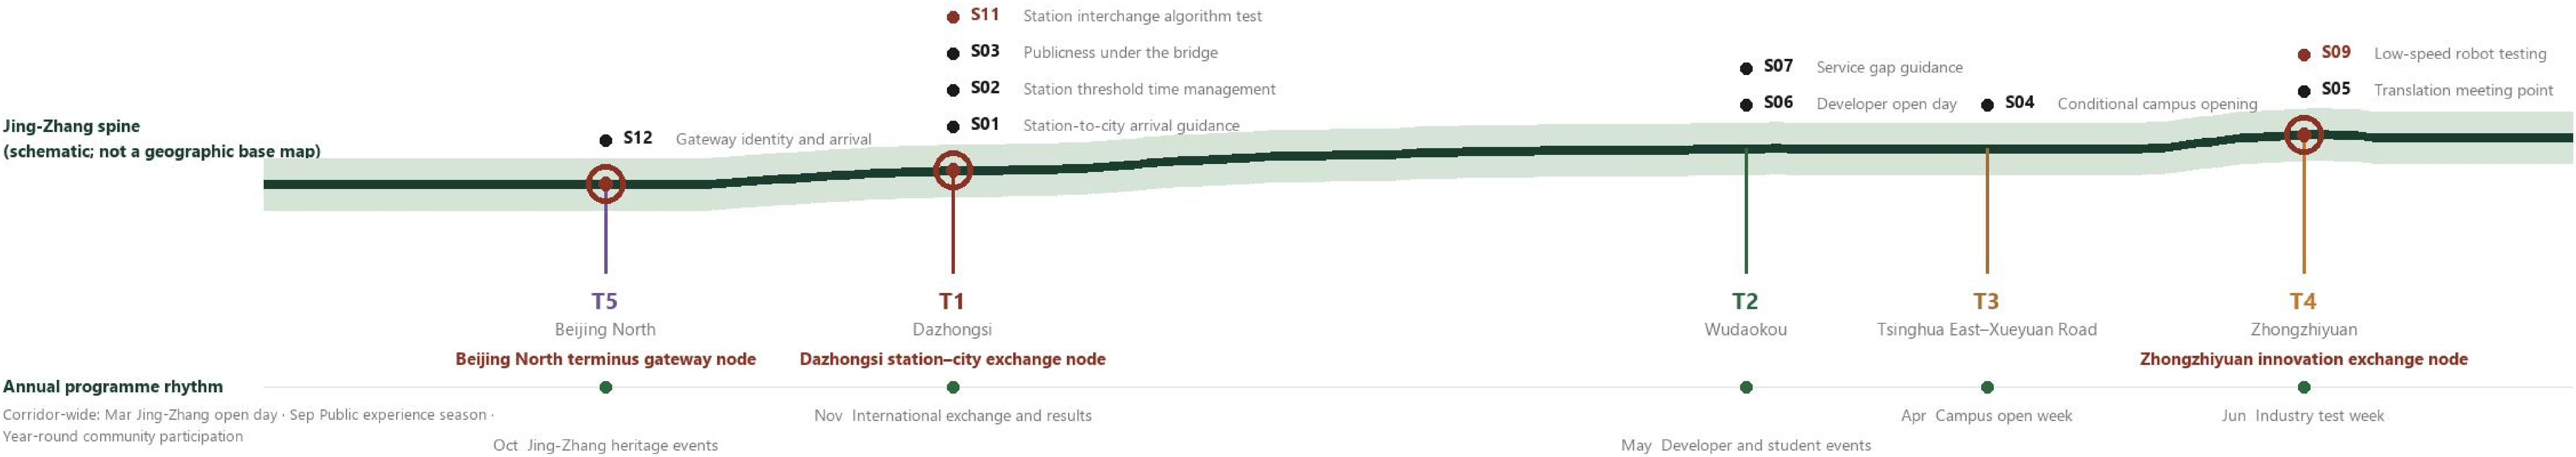

S09 / S10 / S11 are the three industry test-and-verification scenarios (red). All are CONCEPTUAL PROPOSAL / CONDITIONAL; none has obtained data permission; test areas would be publicly notified and manual takeover is always possible.

Four delivery modes | which mode applies where

	T5 Beijing North	T1 Dazhongsì	T2 Wudaokou	T3 Tsinghua East-Xueyuan Road	T4 Zhongzhiyuan
DIRECT DESIGN	Gateway arrival organisation at the station front; east-west link organised through the station area	Extend the entrance-to-spine arrival sequence; organise publicness in the North Third Ring bridge zone	Fill the western access gap (small scale, operation first)	Strengthen publicness at existing crossings	
PLANNING CONTROL	Reserve the Line 13A interface; conditional conversion of the shed land east of the yard	Controlled reconstruction of the renewal parcel and the Lanjing interface	Write interface conditions into the Wudaokou station rebuild	Conditional controlled exchange openings (agreed with the universities)	Conditional green-network interface, northern end-Qinghe
MANAGEMENT / OPERATION		Arrival hours and programme organisation in the 1733 forecourt	Activation of the start-up area · time-shared use		A continuous public interface between industry, green space and everyday space
KEEP / NO DESIGN				KEEP EXISTING CONDITIONS by default: no fence removal, no forced opening	If the crossing condition does not hold → keep existing conditions

Three-phase sequence




The phasing is a conceptual sequence ordered by the priority of relation actions. It is not a development programme, an investment schedule or an approval timetable. No cost, staffing, investment figure, quantity of works or responsible body is proposed; all operating bodies are suggested role categories.

Metrics and compliance begin by stating what evidence each number rests on.

This board is not an audit back end. It gives the verifiable evidence first, then three verifiable diagnoses, and finally states what is verified, what is design-defined and what remains to be verified.

Strongest verifiable evidence

All 24 stations by 800 m coverage (low → high)

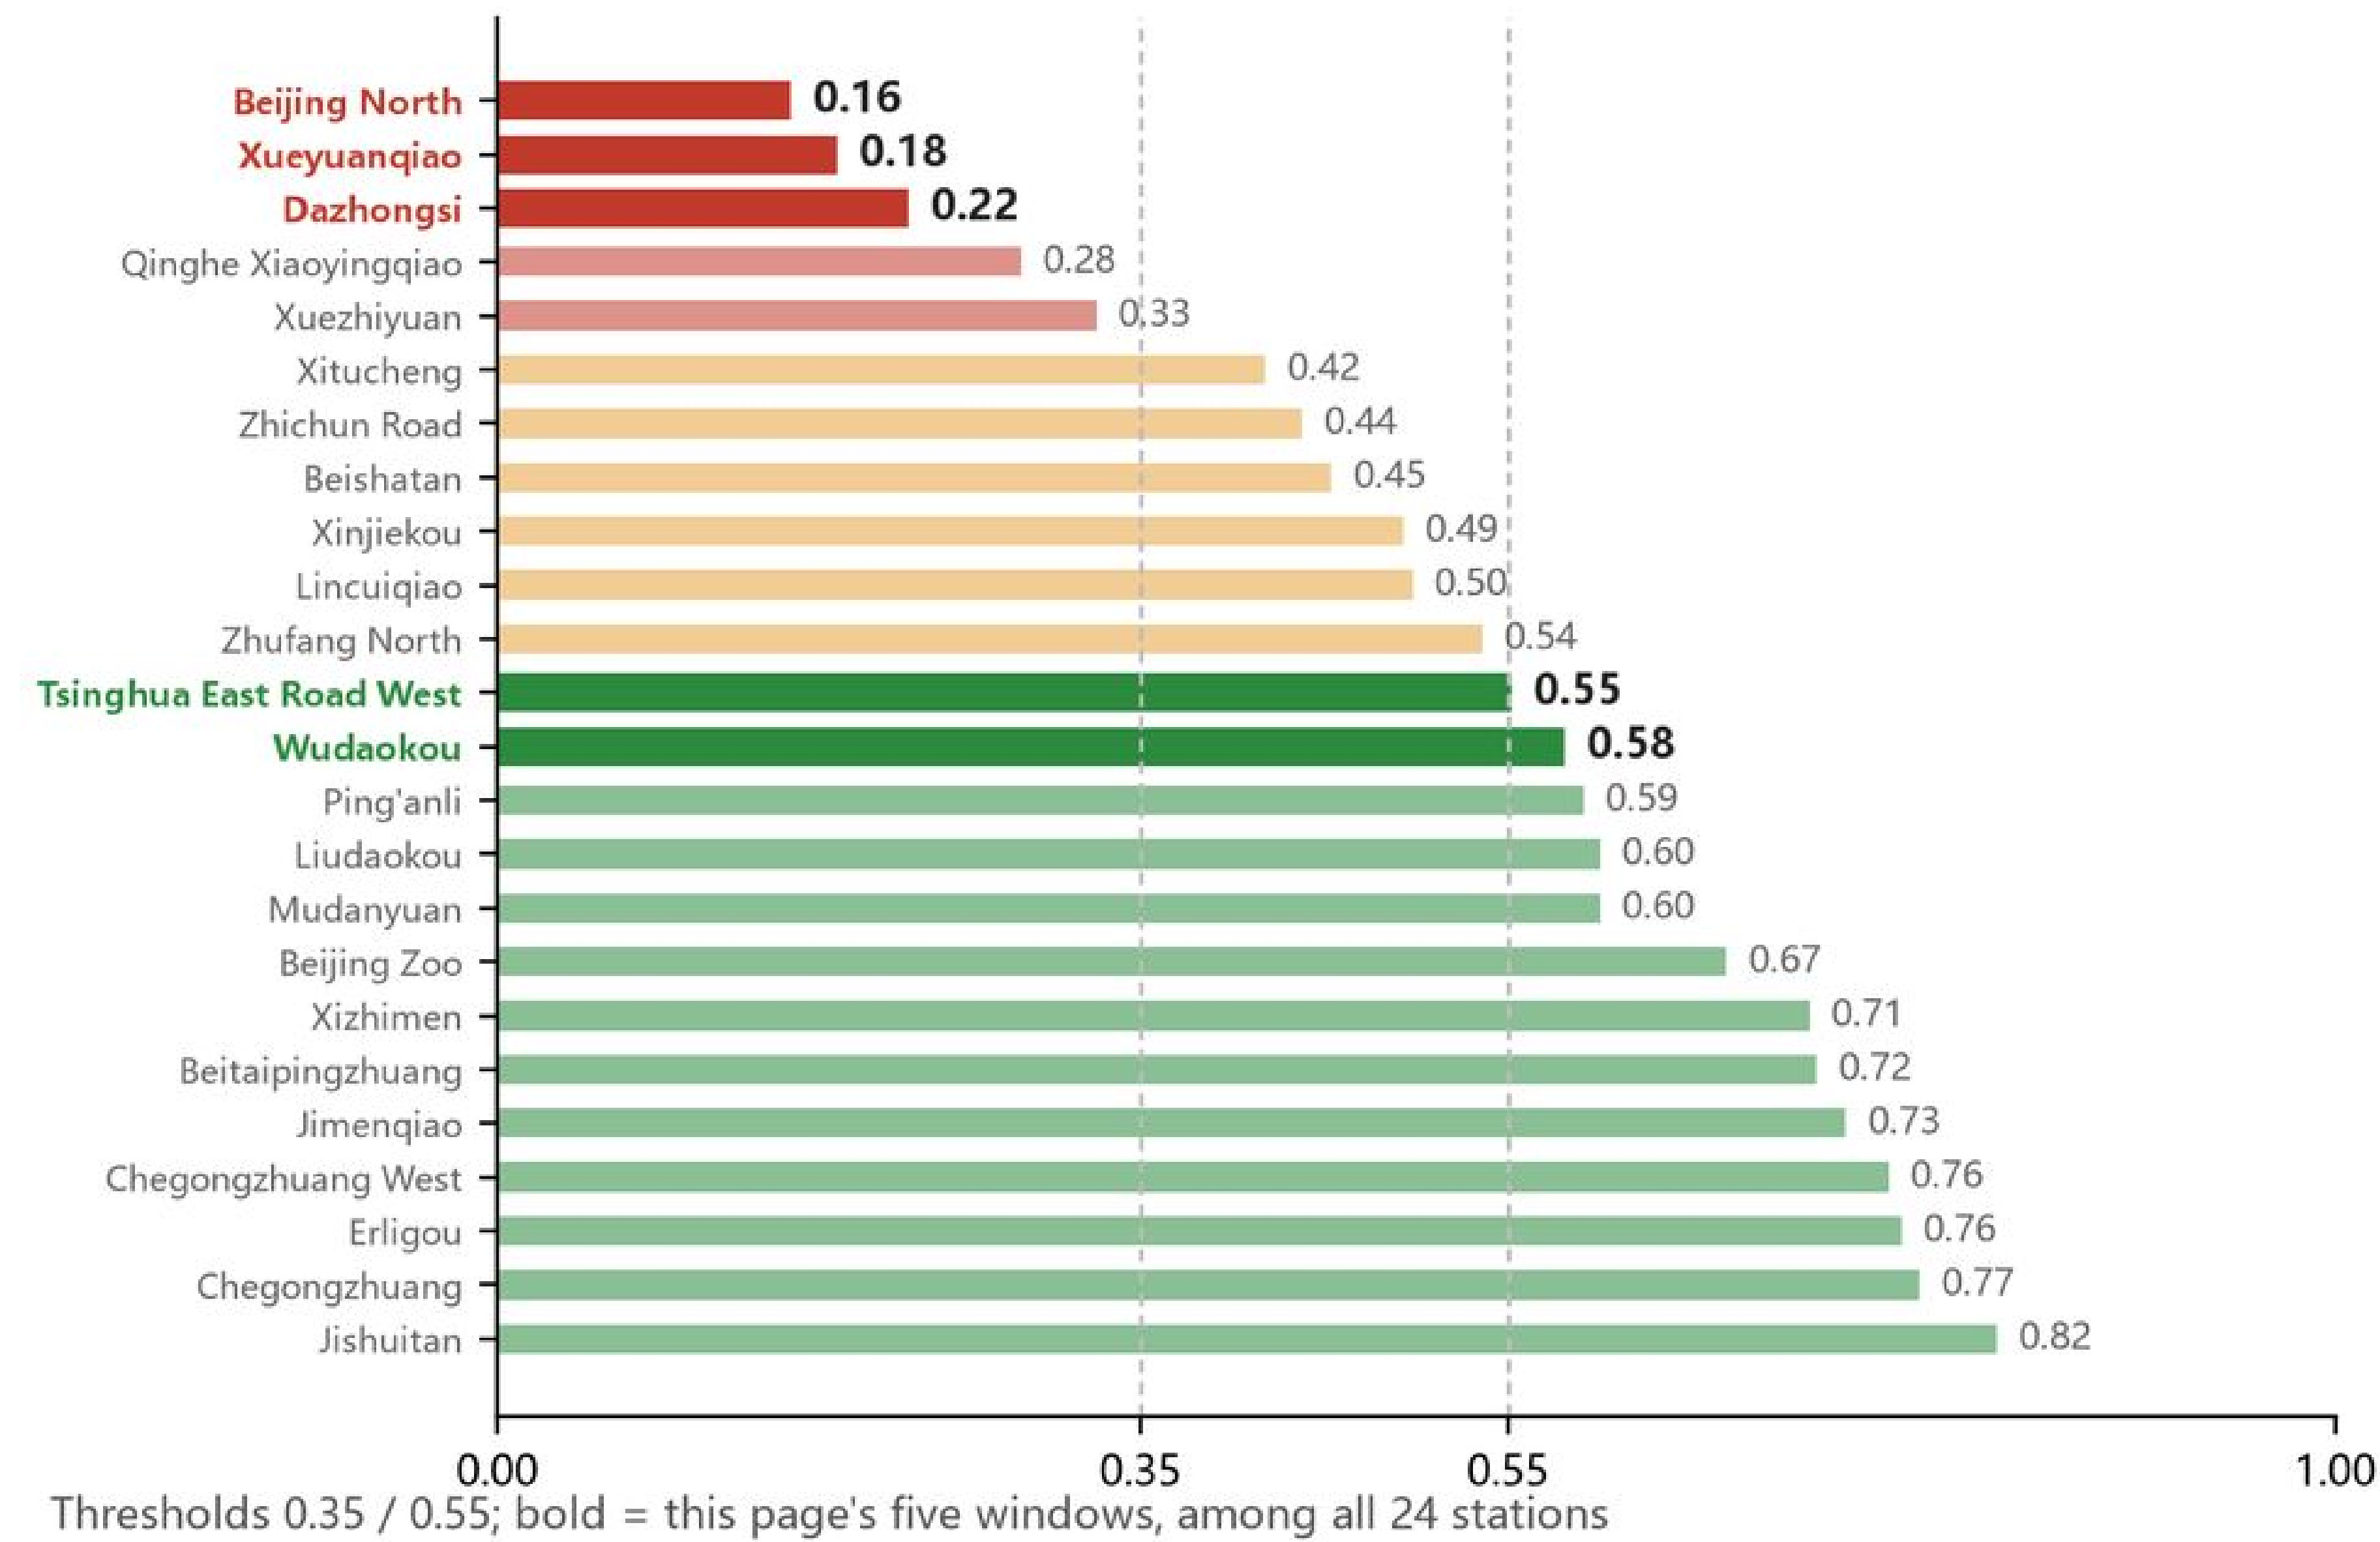

All 24 stations ranked by 800 m coverage | low values concentrate in the southern section and at bridge-zone stations.

Status boundaries

VERIFIED

800 m network coverage per station (own indicator) · classification of the seven existing crossings · park entrances and share of negative interface · plan-level factual relations at T1 (1733 / Entrances A-B / station structure / Line 13 / Jing-Zhang / North Third Ring)

DESIGN-DEFINED

Forecourt arrival · public hinge within the station · upper-level public transfer · heritage park interface · opening locations of the conditional controlled exchange interface

TO VERIFY

Exact levels · vertical circulation within the station structure · engineering interfaces · landing conditions of N2 · headroom and structure under the bridge · opening hours and rules of each university

NOT PROPOSED AT THIS STAGE

Any unverified new rail crossing · statutory land-use change · retain/renovate/demolish judgement · plot ratio and building height control

Compliance coverage

✓ Three-scale scope

A0-01

✓ Three key areas

A0-05

✓ Mobility and blue-green

A0-03 / A0-04

✓ AI scenarios

A0-06

✓ Delivery and operation


A0-06

✓ Metrics recomputation

A0-07

Evidence for the three diagnoses is on the left of this board and on A0-03 / A0-04. Once the official redline and the formal boundaries of the three key areas are released, the extents and statistics must be recomputed in full.

Provisional submission extent: about 11.41 km². This is the extent recorded in the submission package and is not a design-performance indicator.

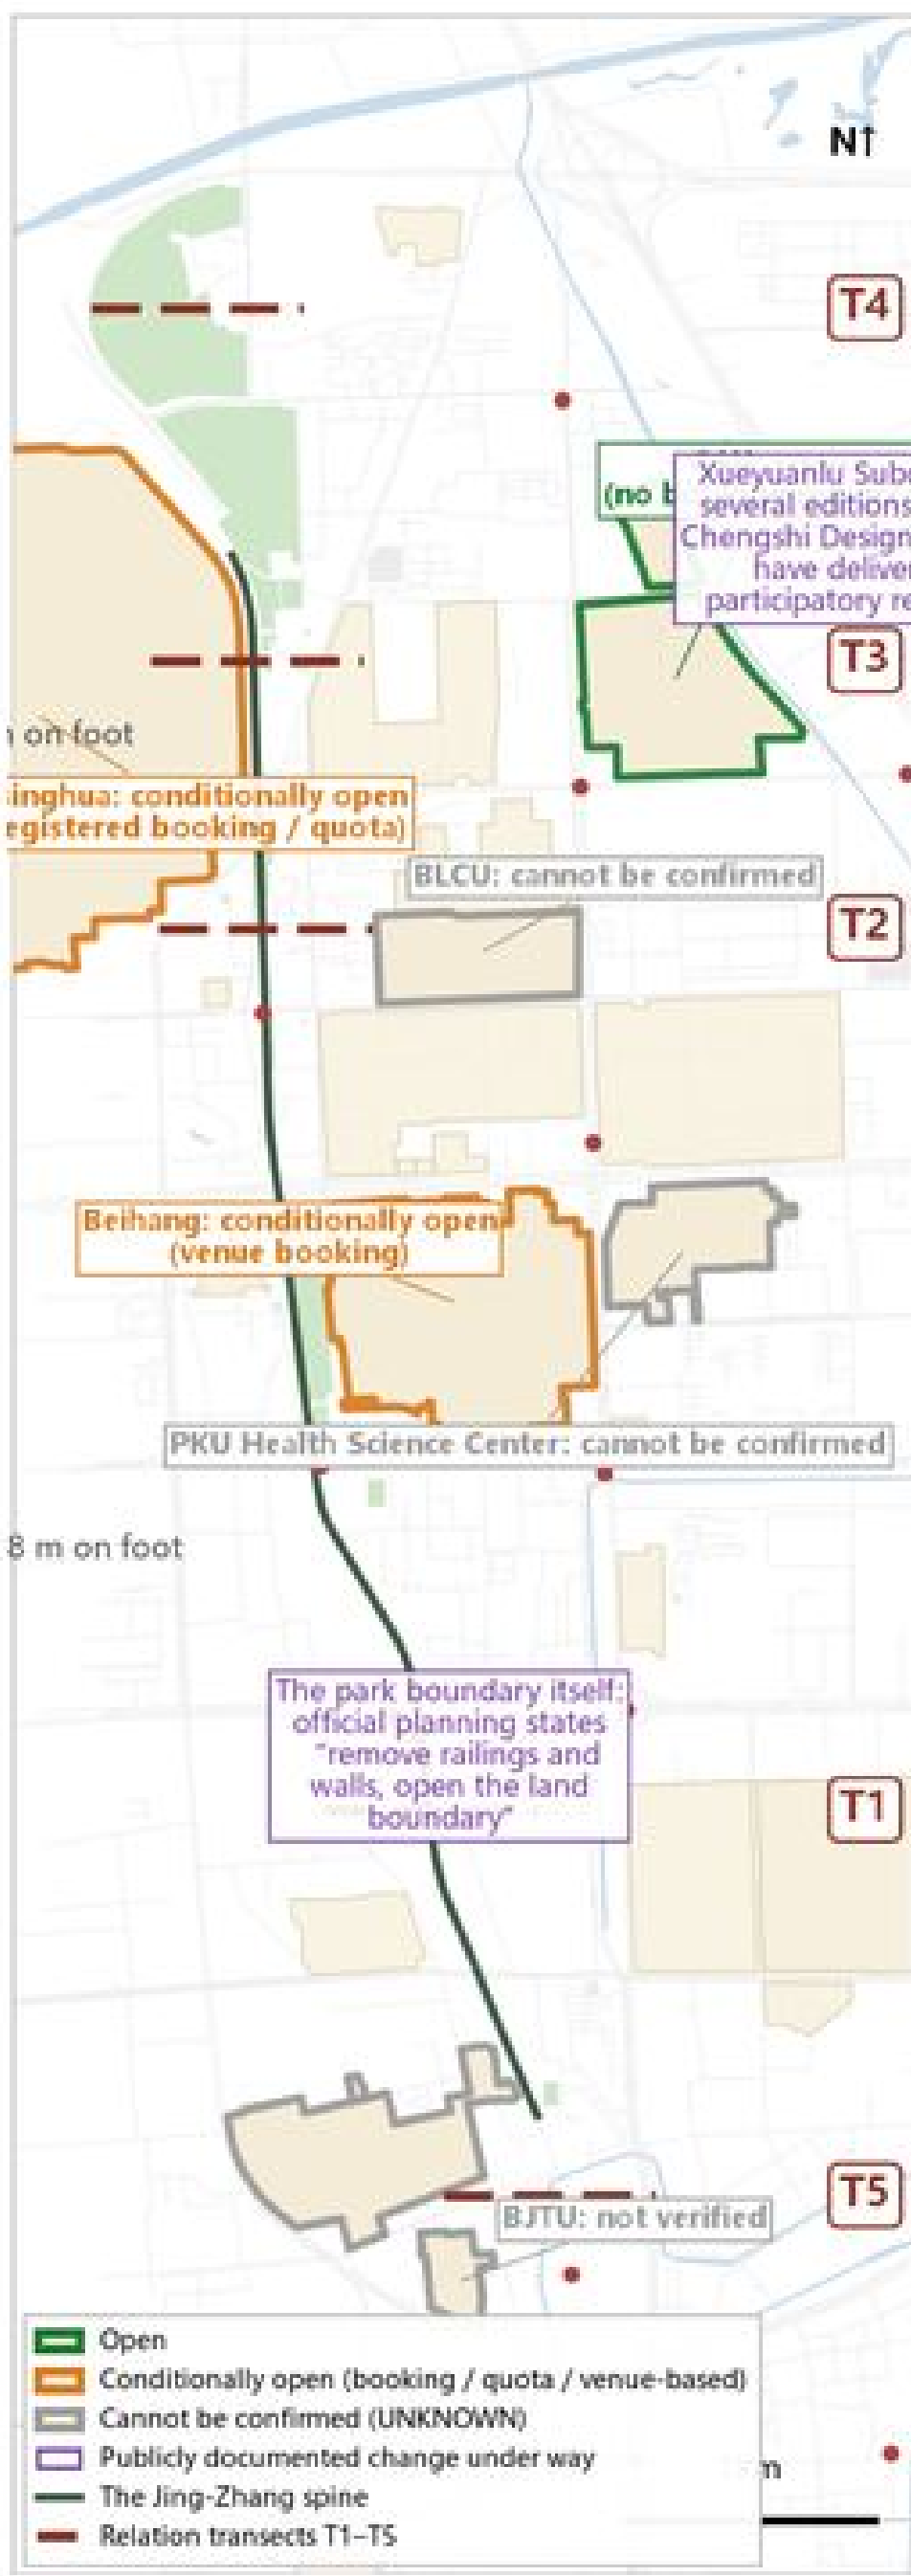

Campus openness | Open / Conditionally open / Cannot be confirmed.



Residential node → nearest registered park entrance | green ≤400 m / amber ≤1,200 m / red >1,200 m.

Three Verifiable Diagnoses

01 | Real access to stations

800 m real coverage across 24 stations: 0.16–0.82

Beijing North 0.16 · Xueyuanqiao 0.18 · Dazhongsi 0.22

A Station ≠ Real Access

02 | Proximity-to-access gap

About 97 m to the park edge / about 700 m to the nearest entrance

Walked verification on the Zhichun Road segment (same stretch, same network)

Spatial Proximity ≠ Easy Access — a gap of about 7.2×

03 | Ecological continuity to public use

Five structural breaks, four of them linked to grey infrastructure

Residential node to park entrance: walked / straight-line ratio about 1.4–3.7× (sample)

Ecological Continuity ≠ Continuous Public Use

Plot ratio, building height control and the number of retain/renovate/demolish parcels remain undetermined: the official regulatory plan and redline are not public, and no design-model value is substituted for a statutory indicator.